


# Первинний план

Умовні позначення:


- Існуюча стіна
- Тримальна колона

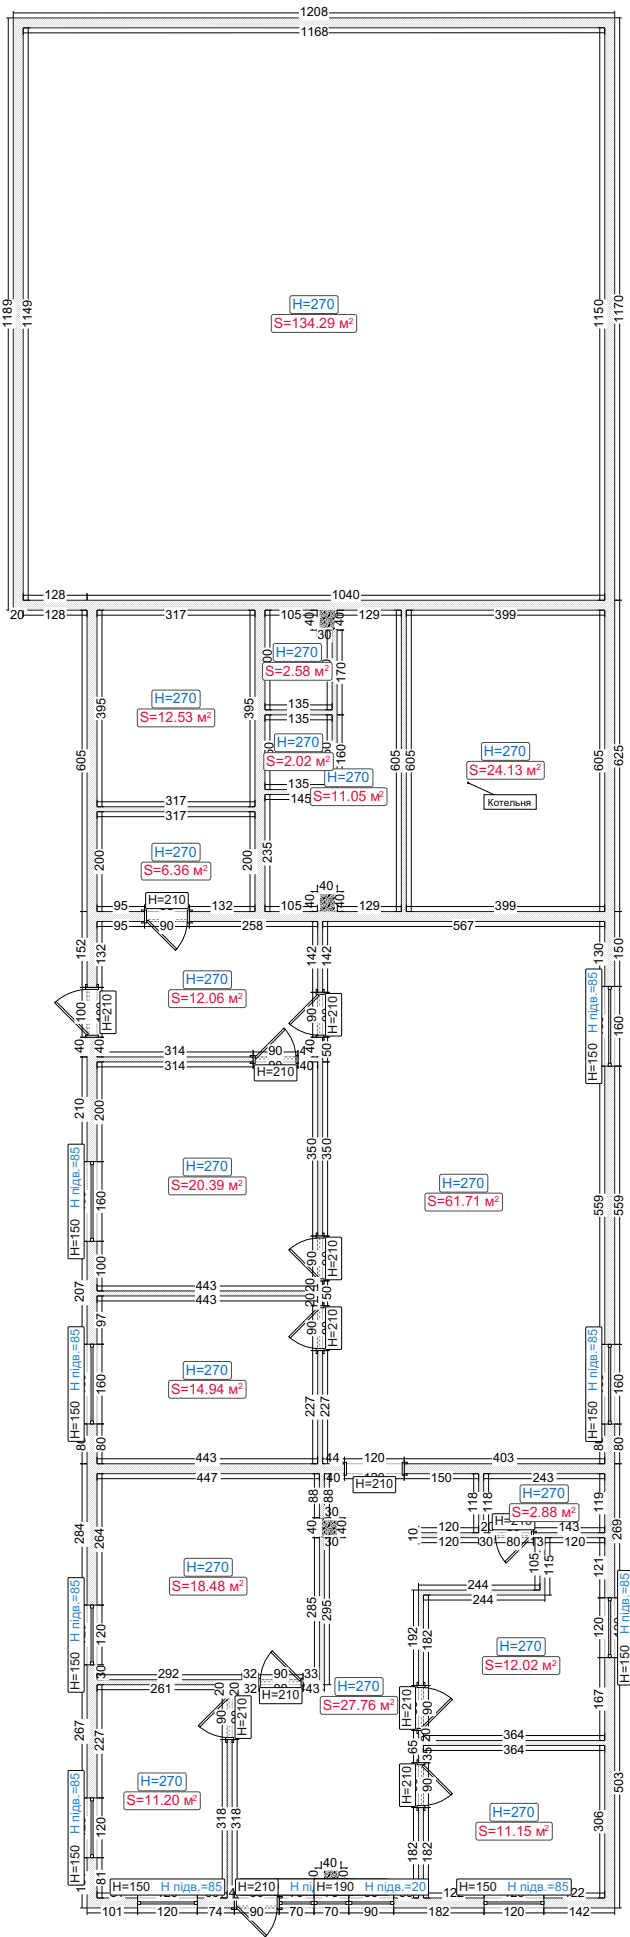

# Демонтаж

Умовні позначення:


 Демонтаж

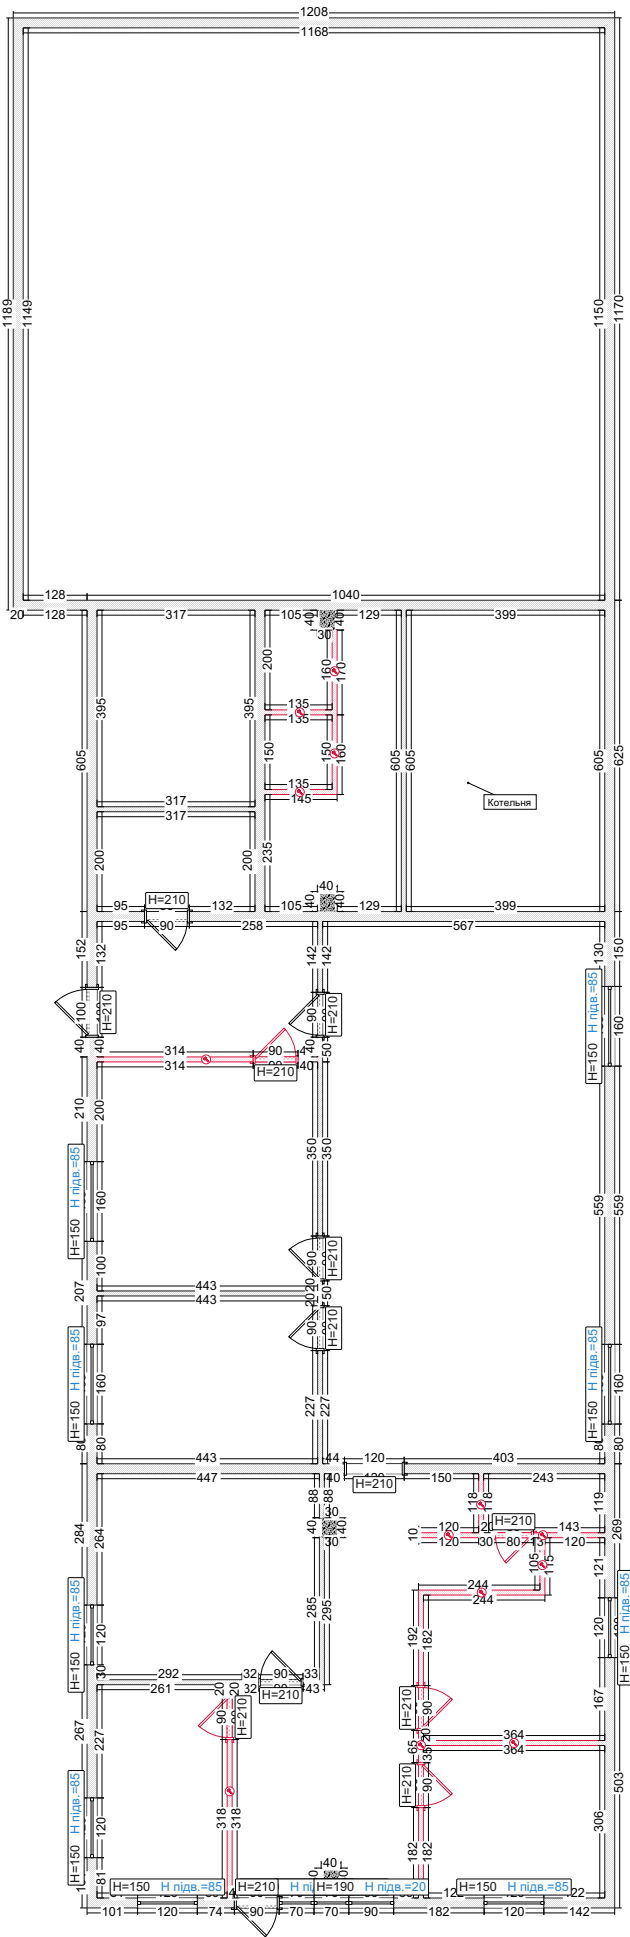



# Перегородка


Умовні позначення:

Стіна з ПГБ

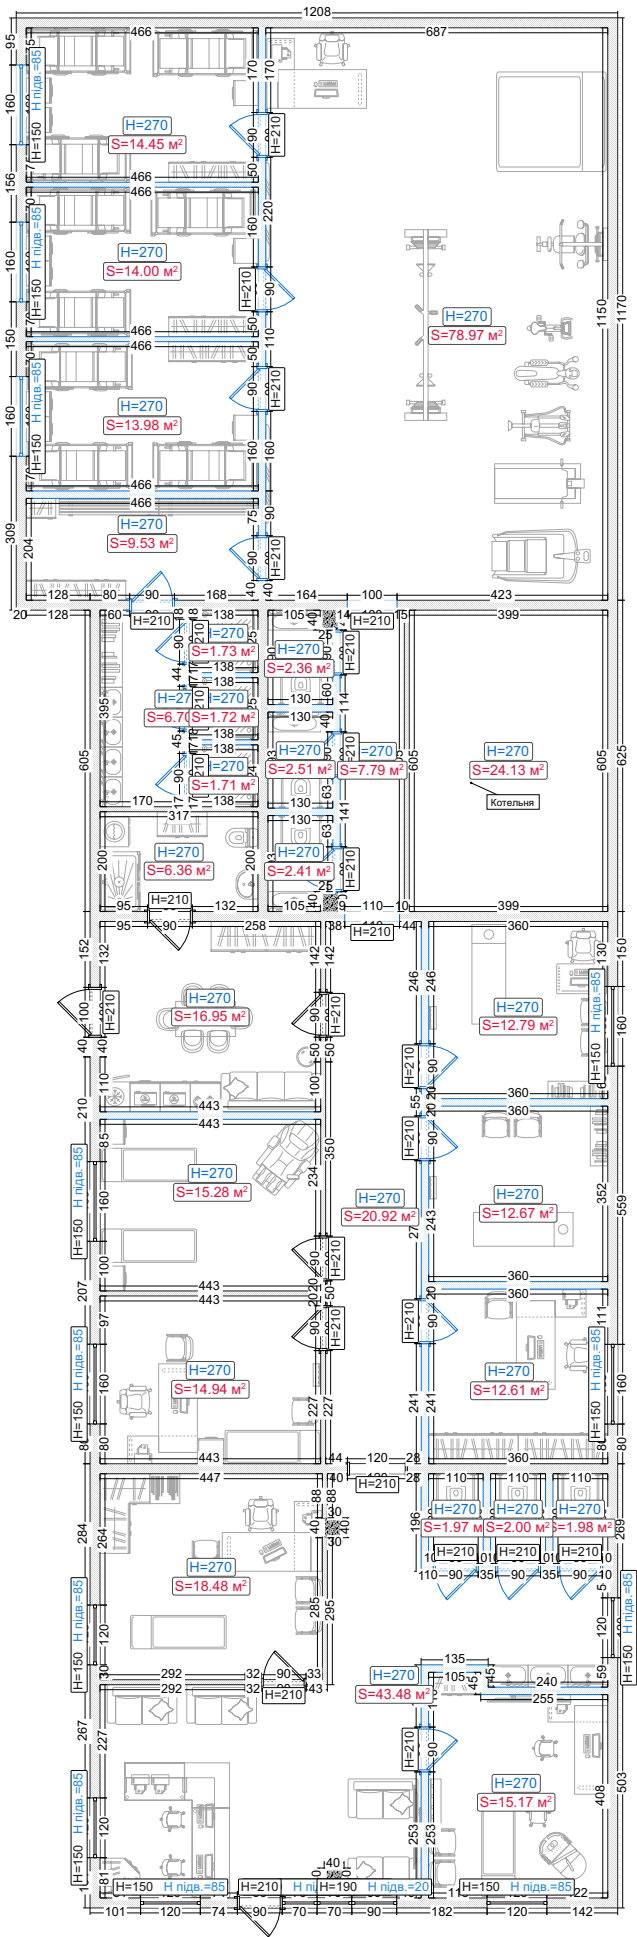


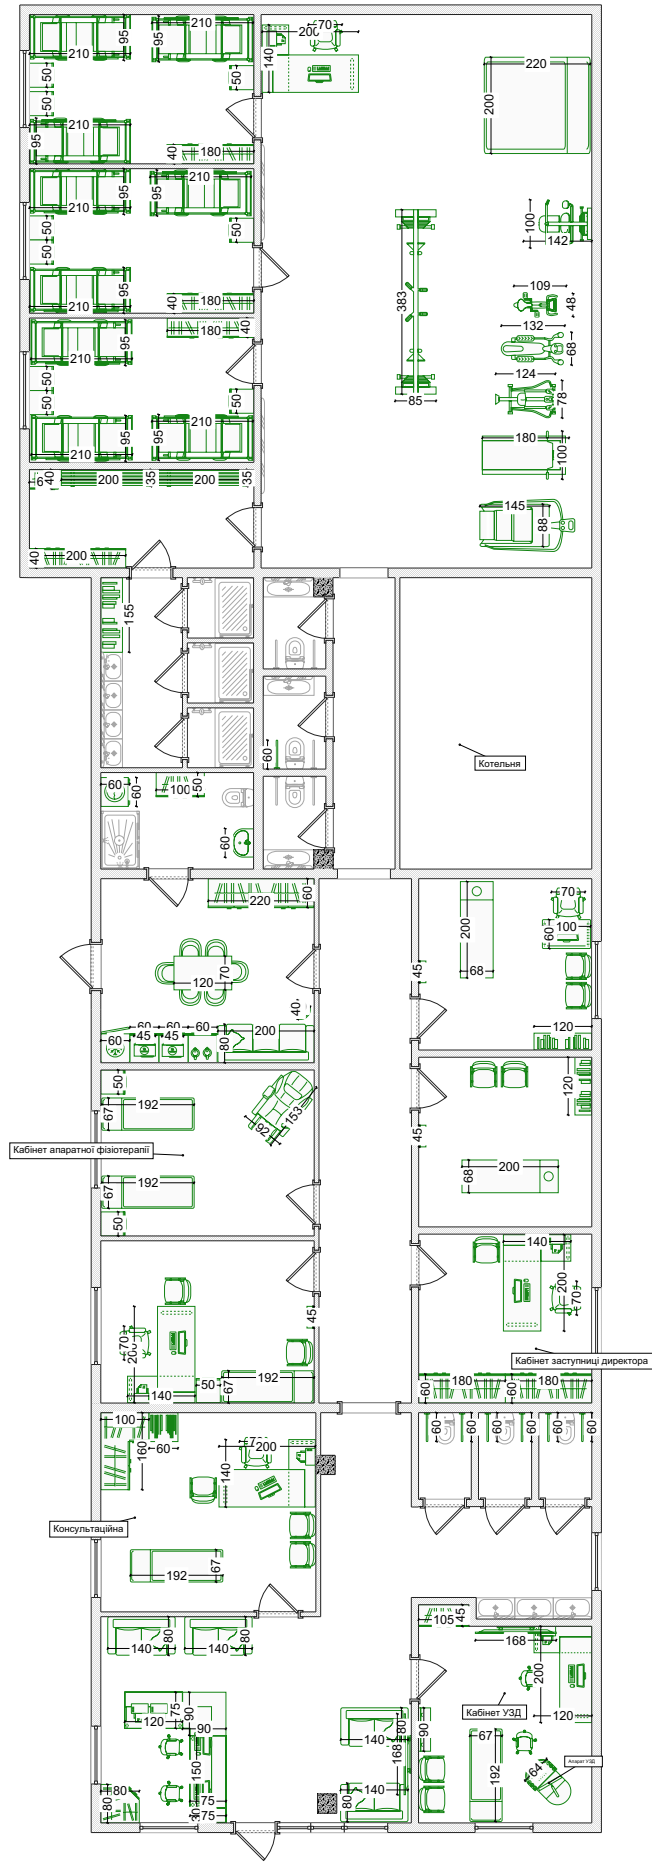


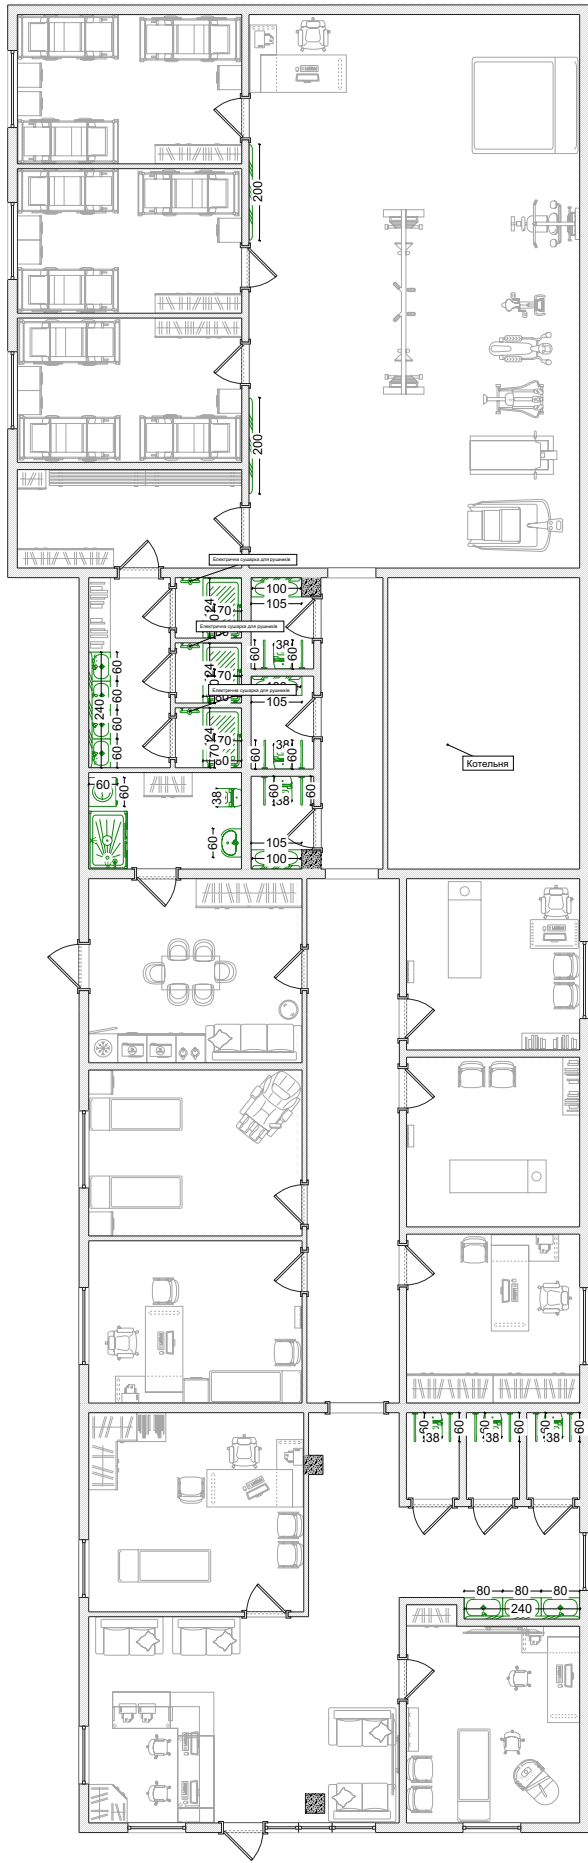


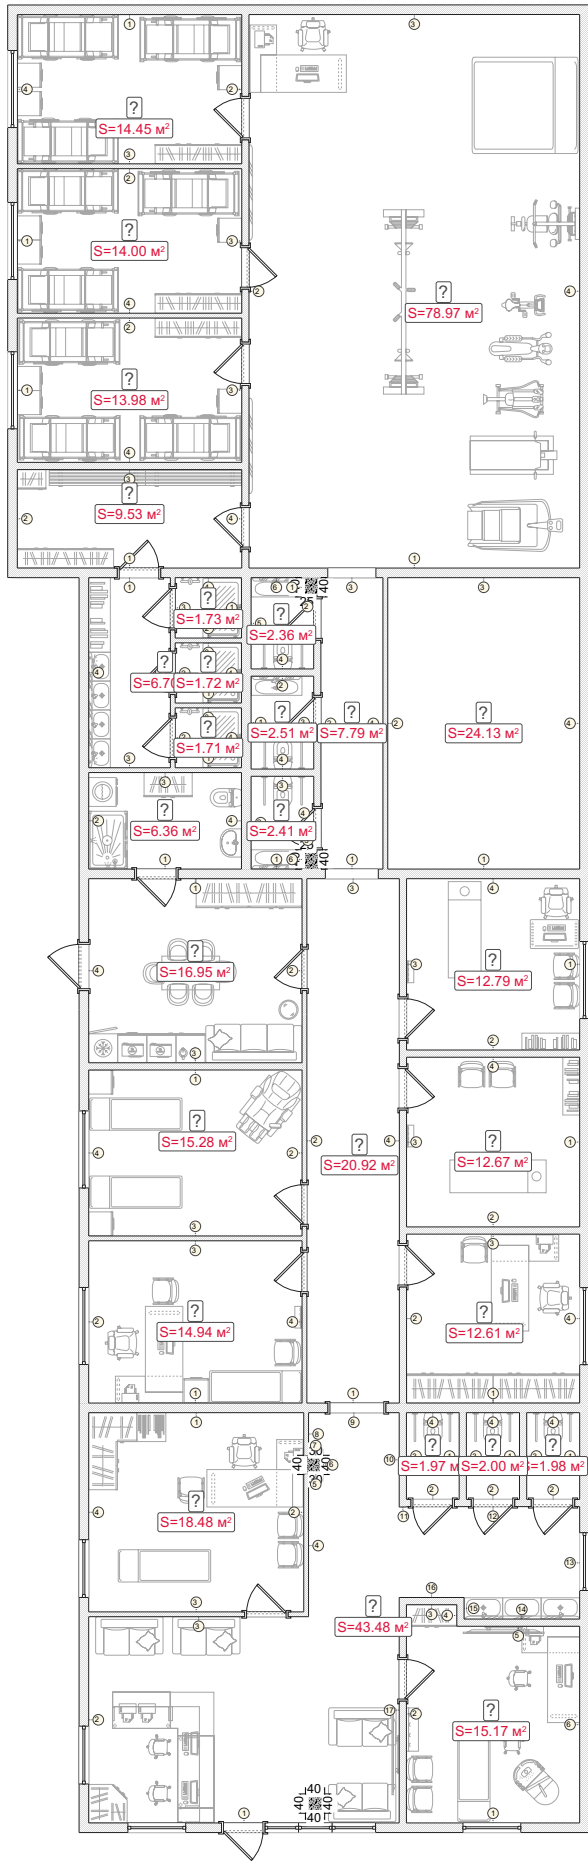






Розгортки стін. Приміщення без назви (1-2)

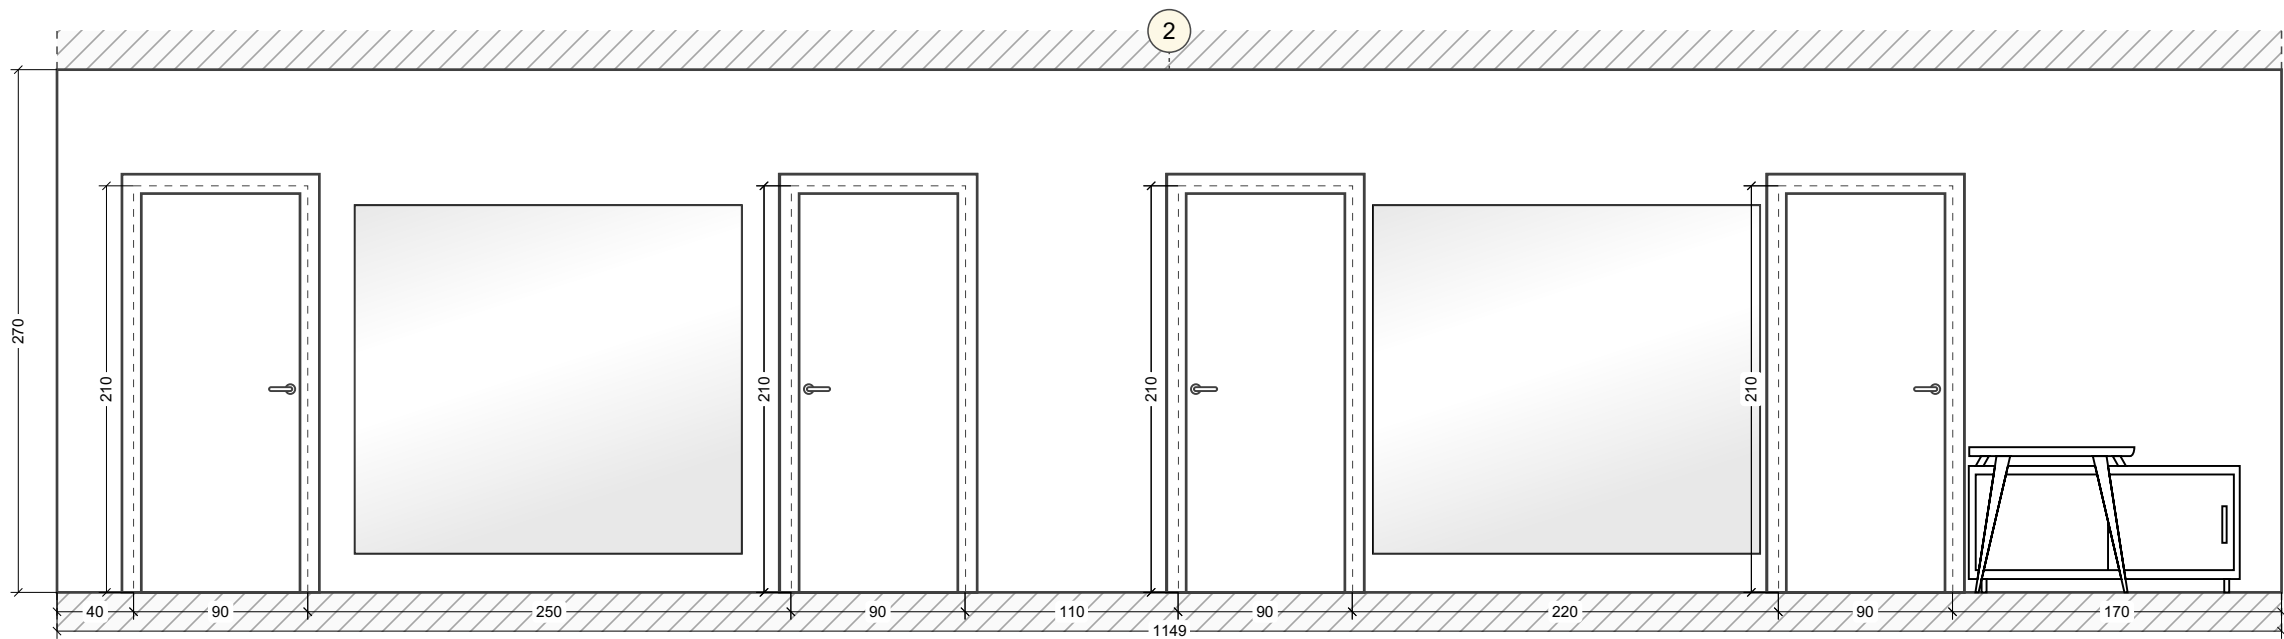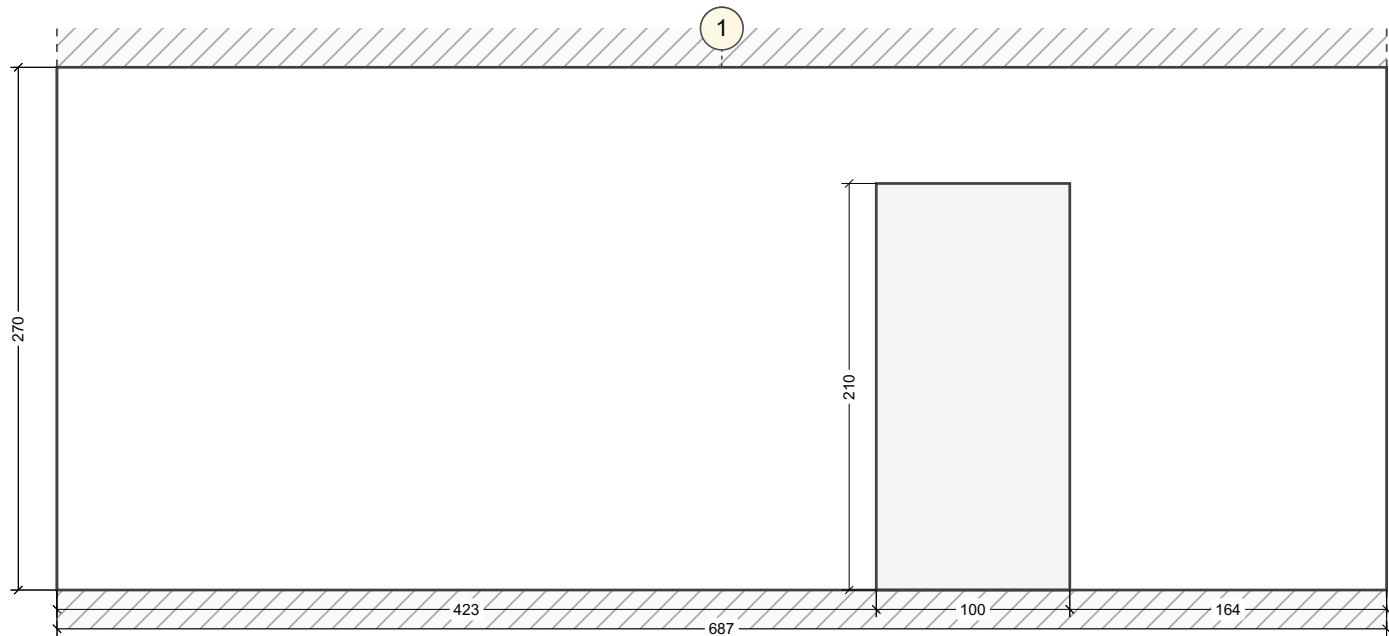


Розгортки стін. Приміщення без назви (3-4)

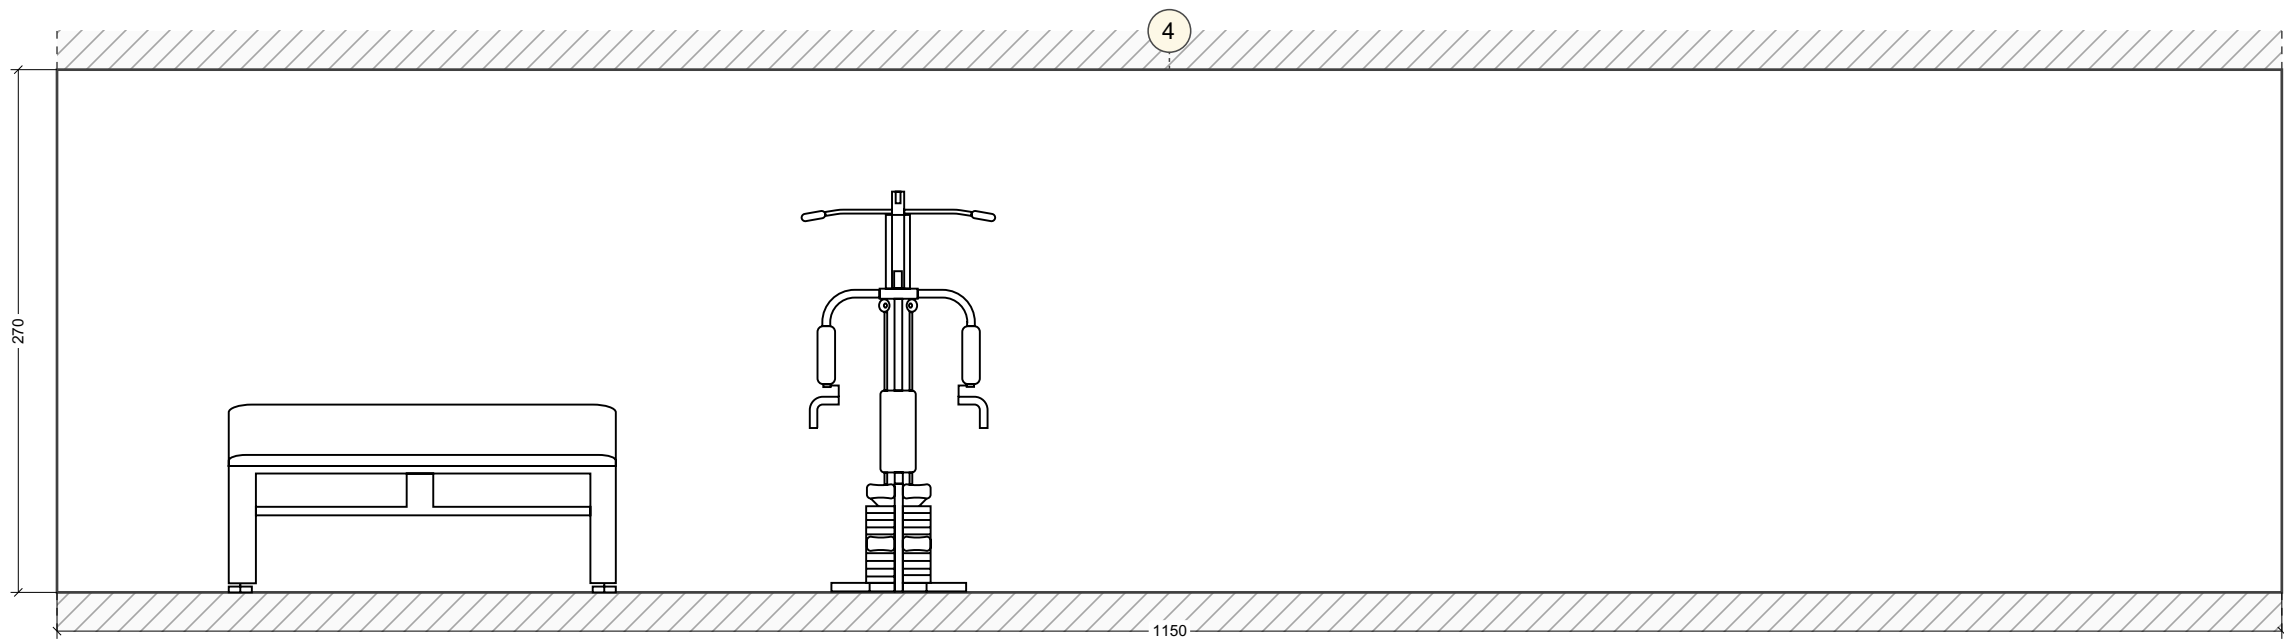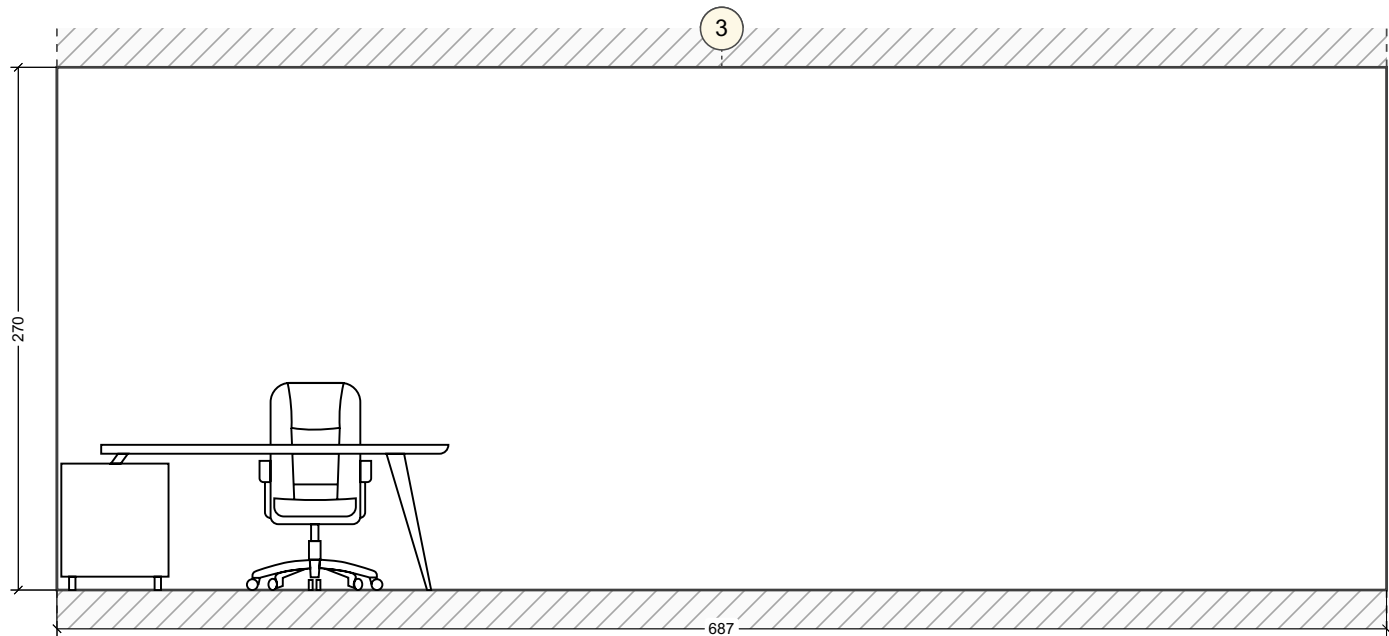





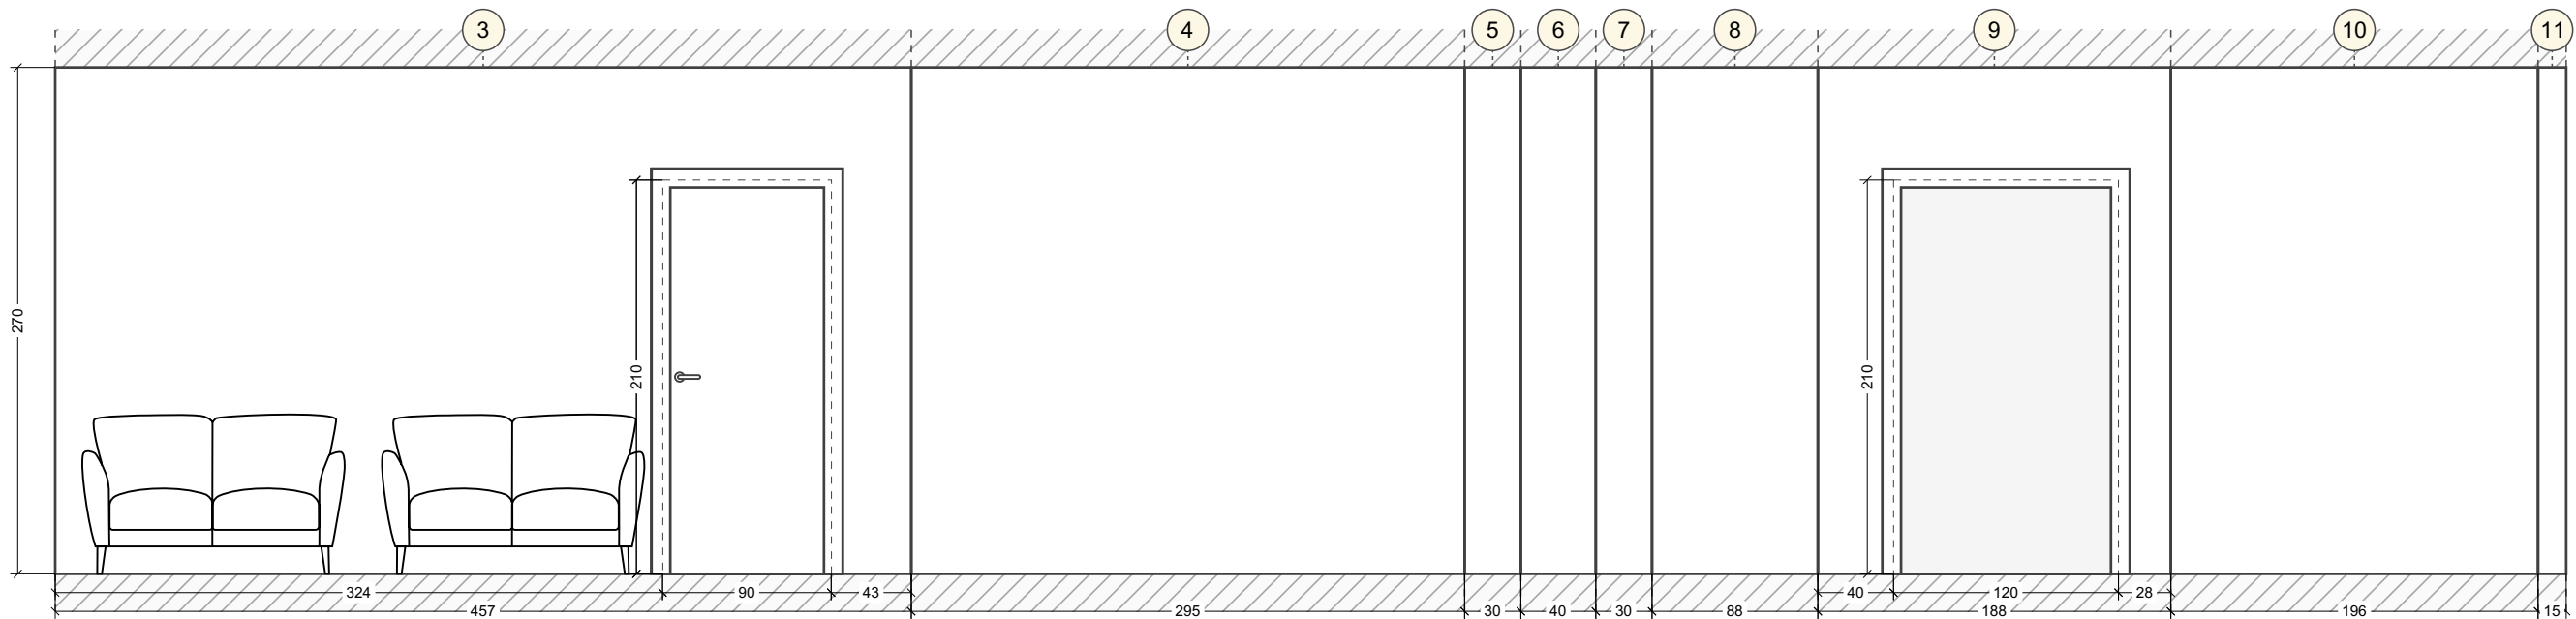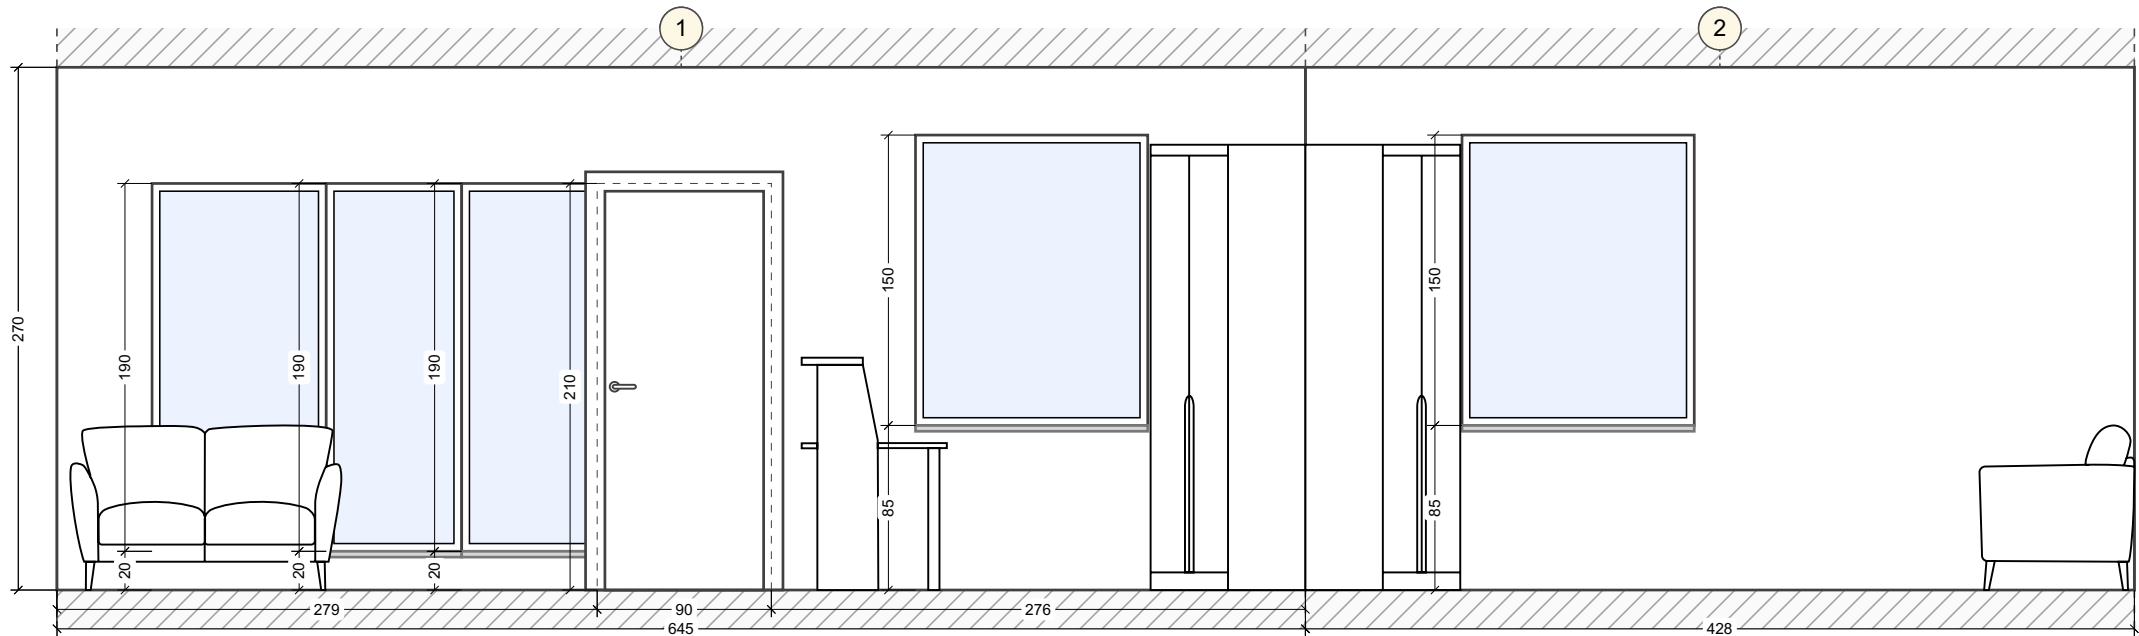



Розгортки стін. Приміщення без назви (12-17)

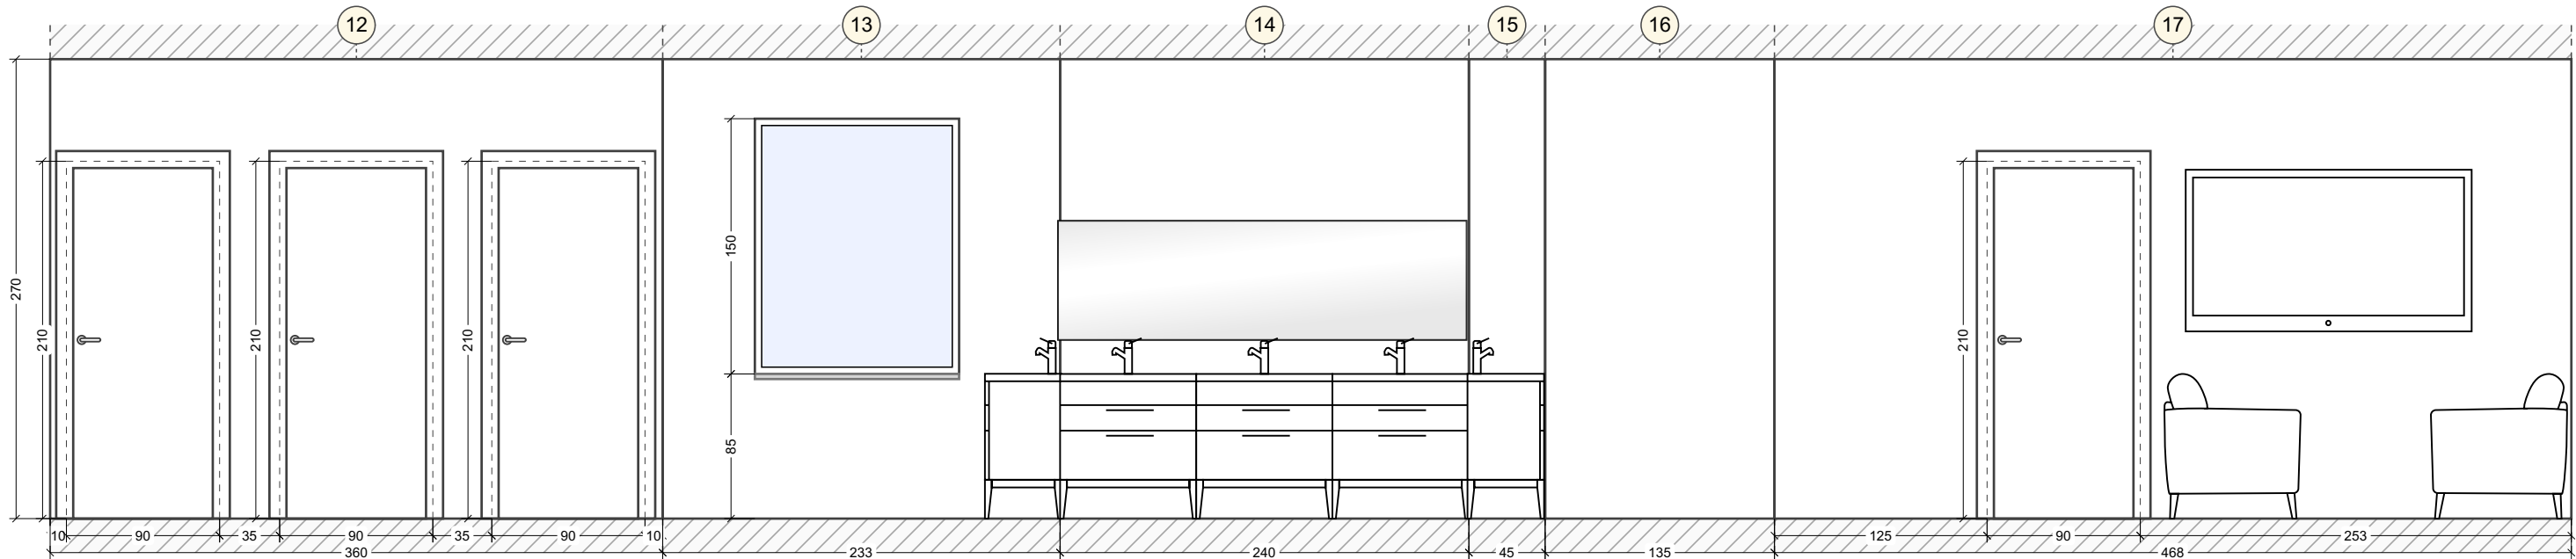



Розгортки стін. Приміщення без назви (1-4)

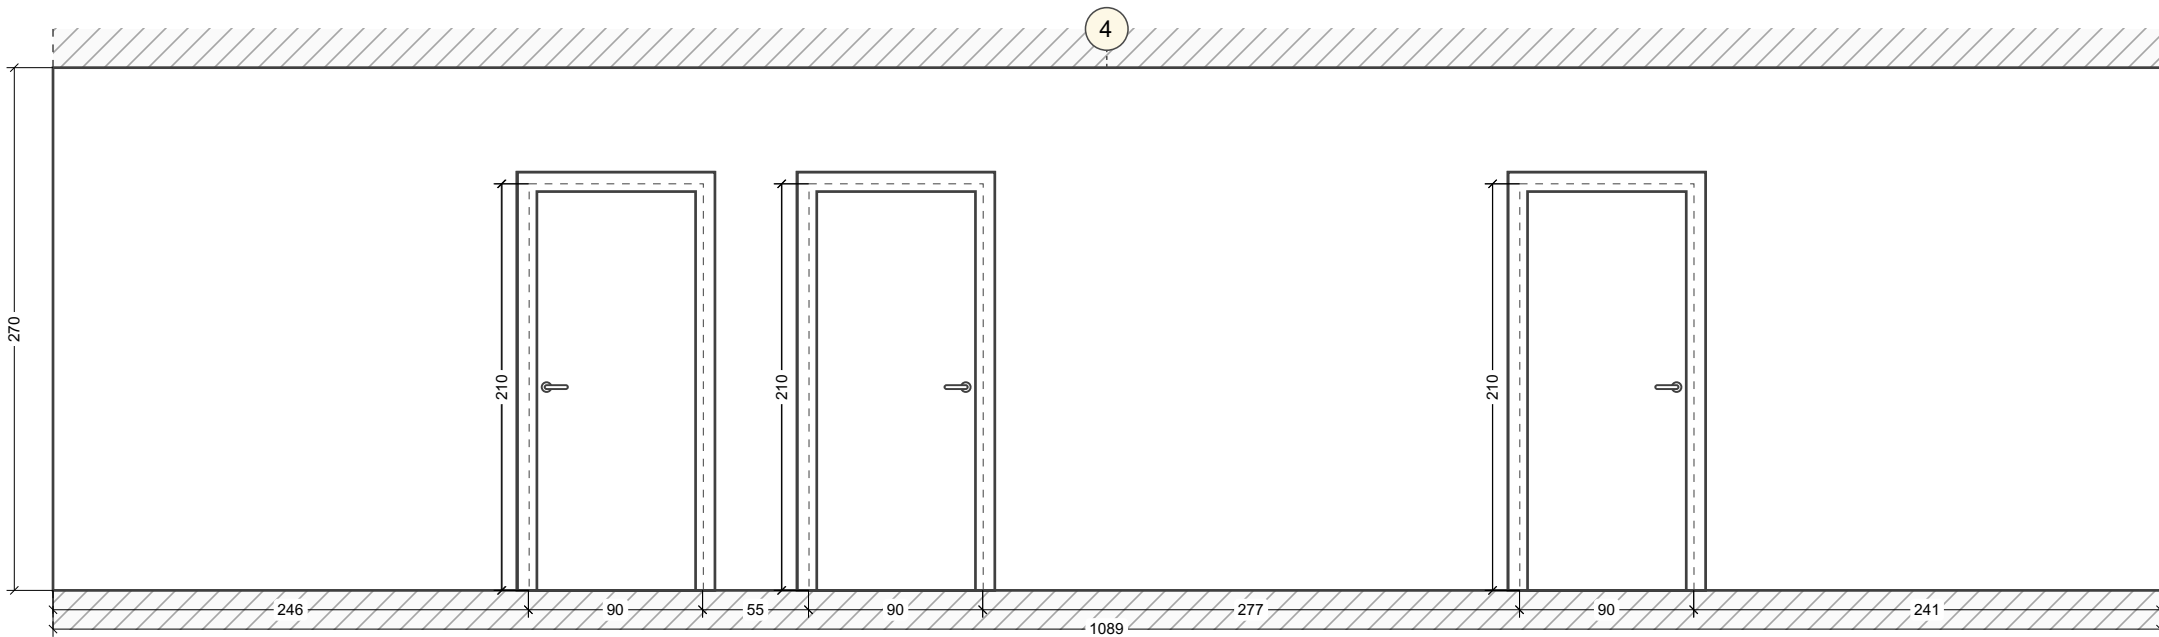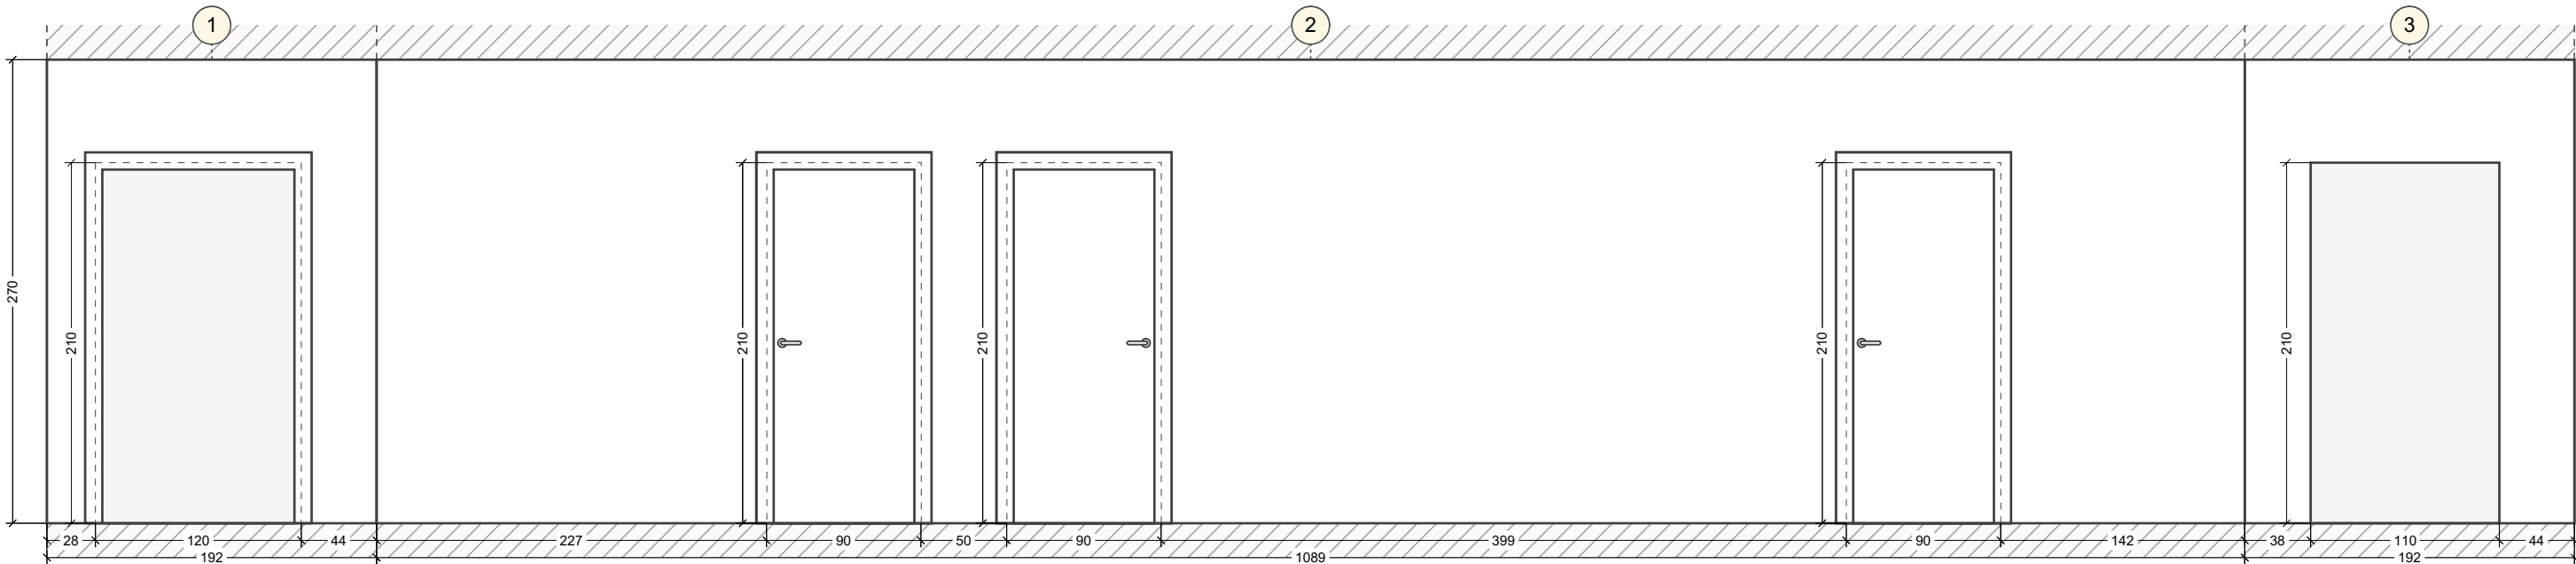



Розгортки стін. Приміщення без назви (1-4)

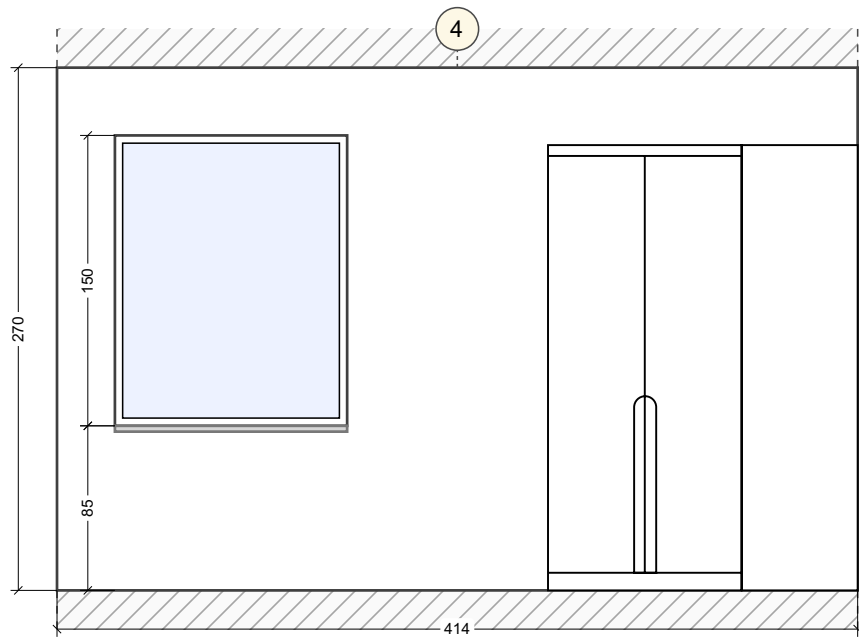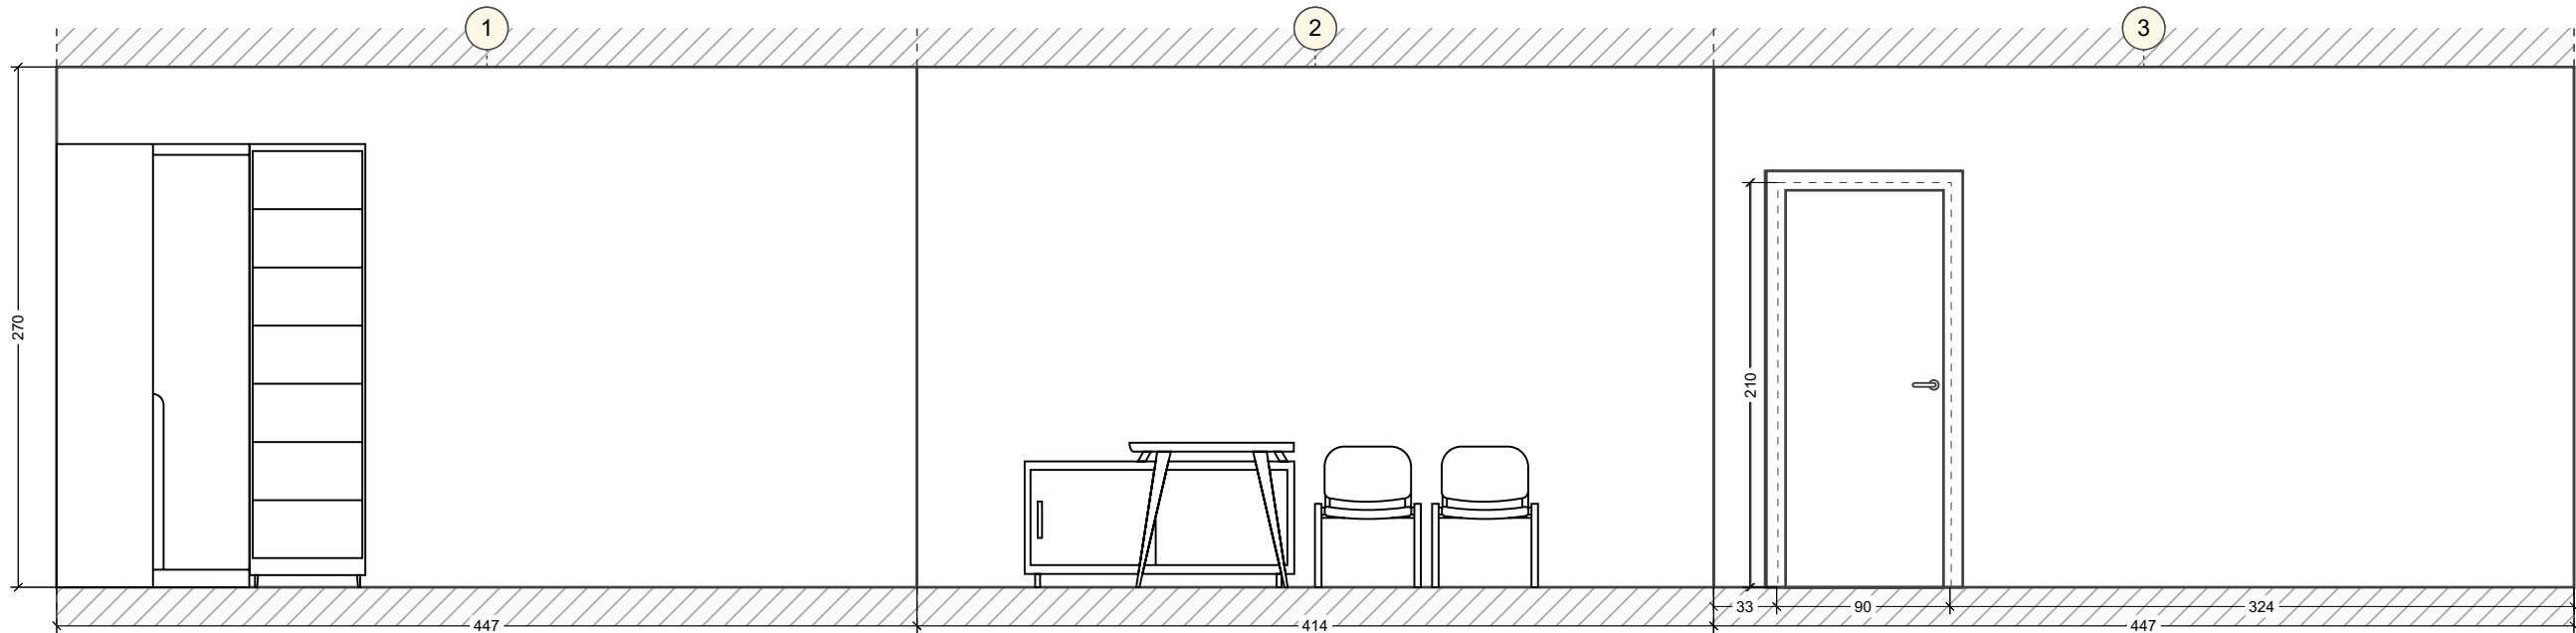

Розгортки стін. Приміщення без назви (1-4)

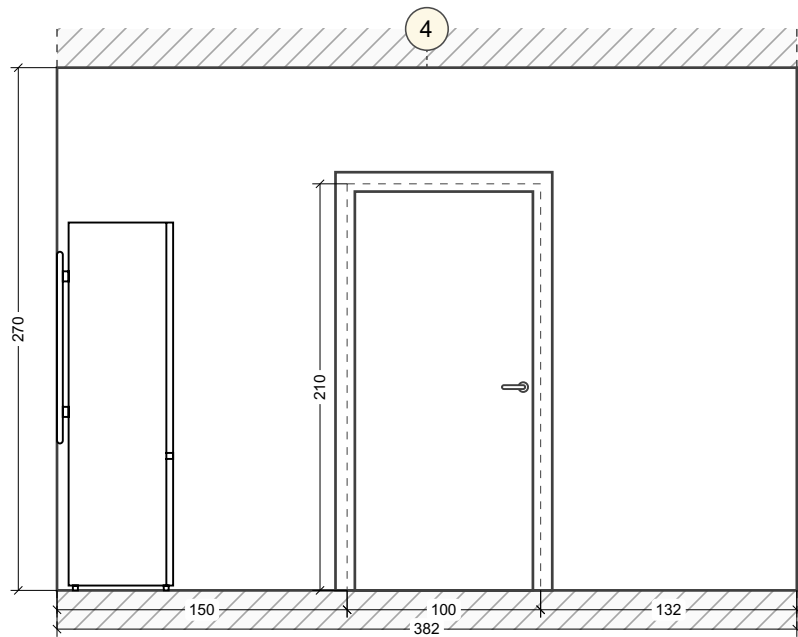
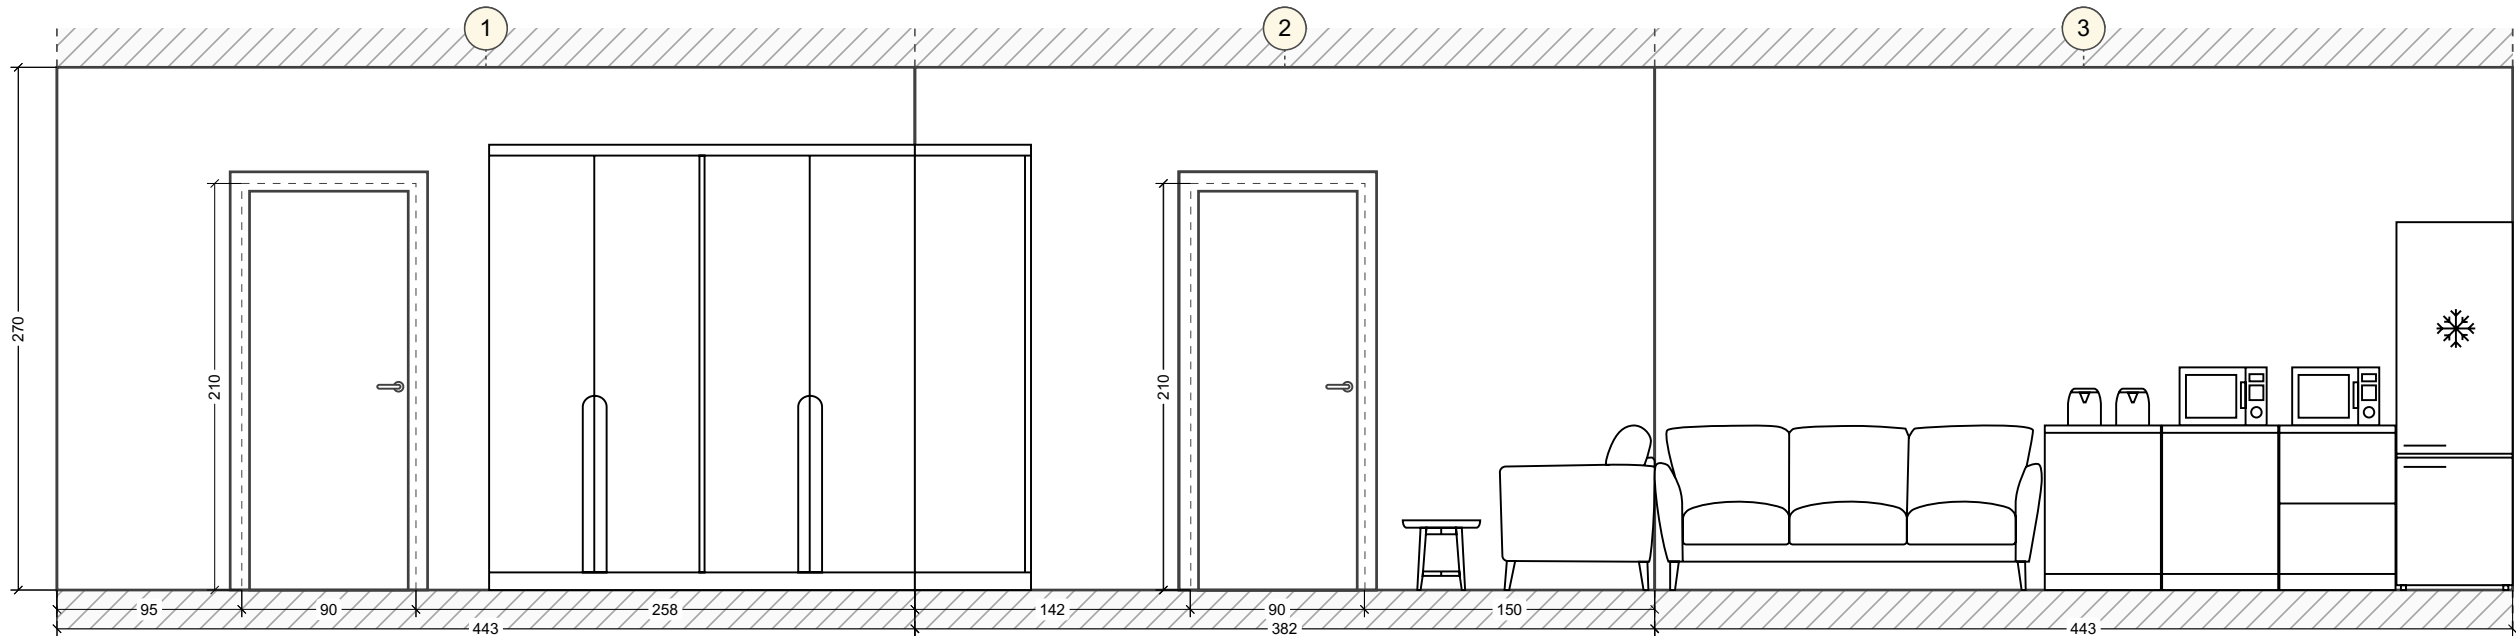


Розгортки стін. Приміщення без назви (1-4)

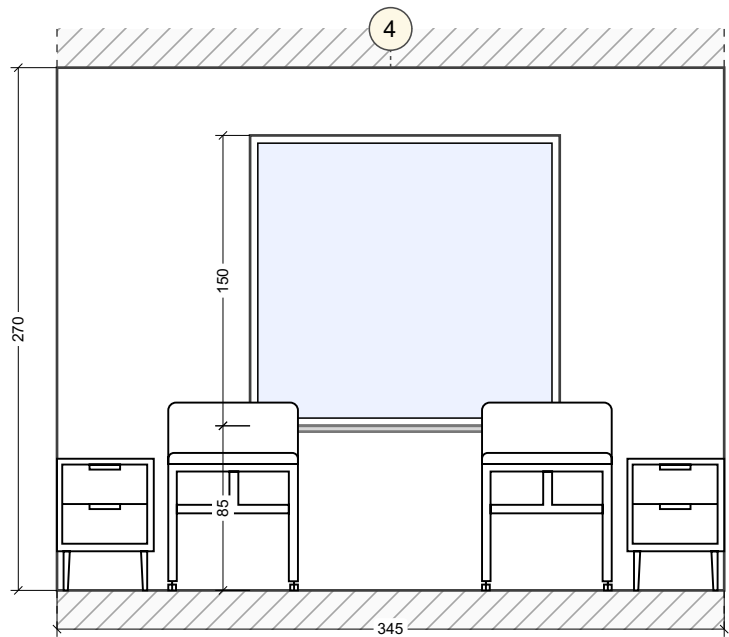
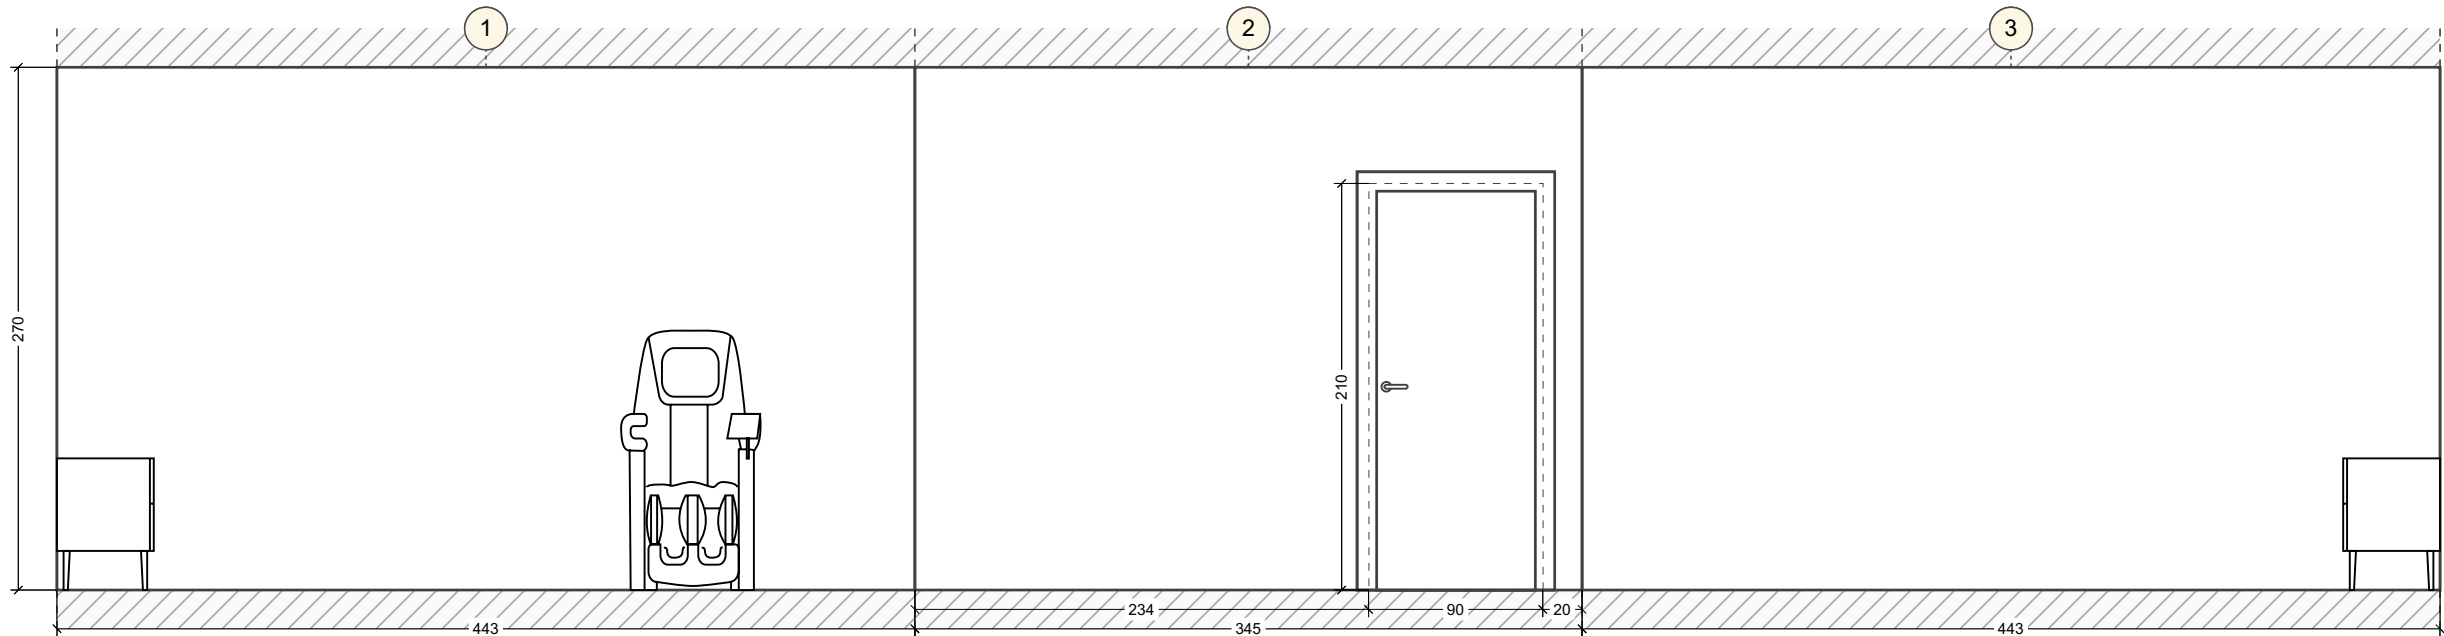




Розгортки стін. Приміщення без назви (1-6)

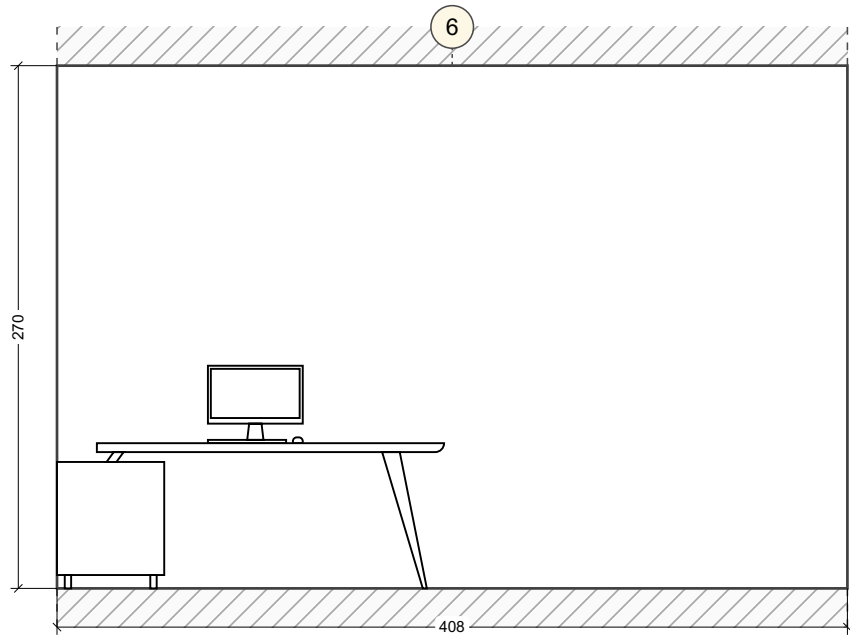
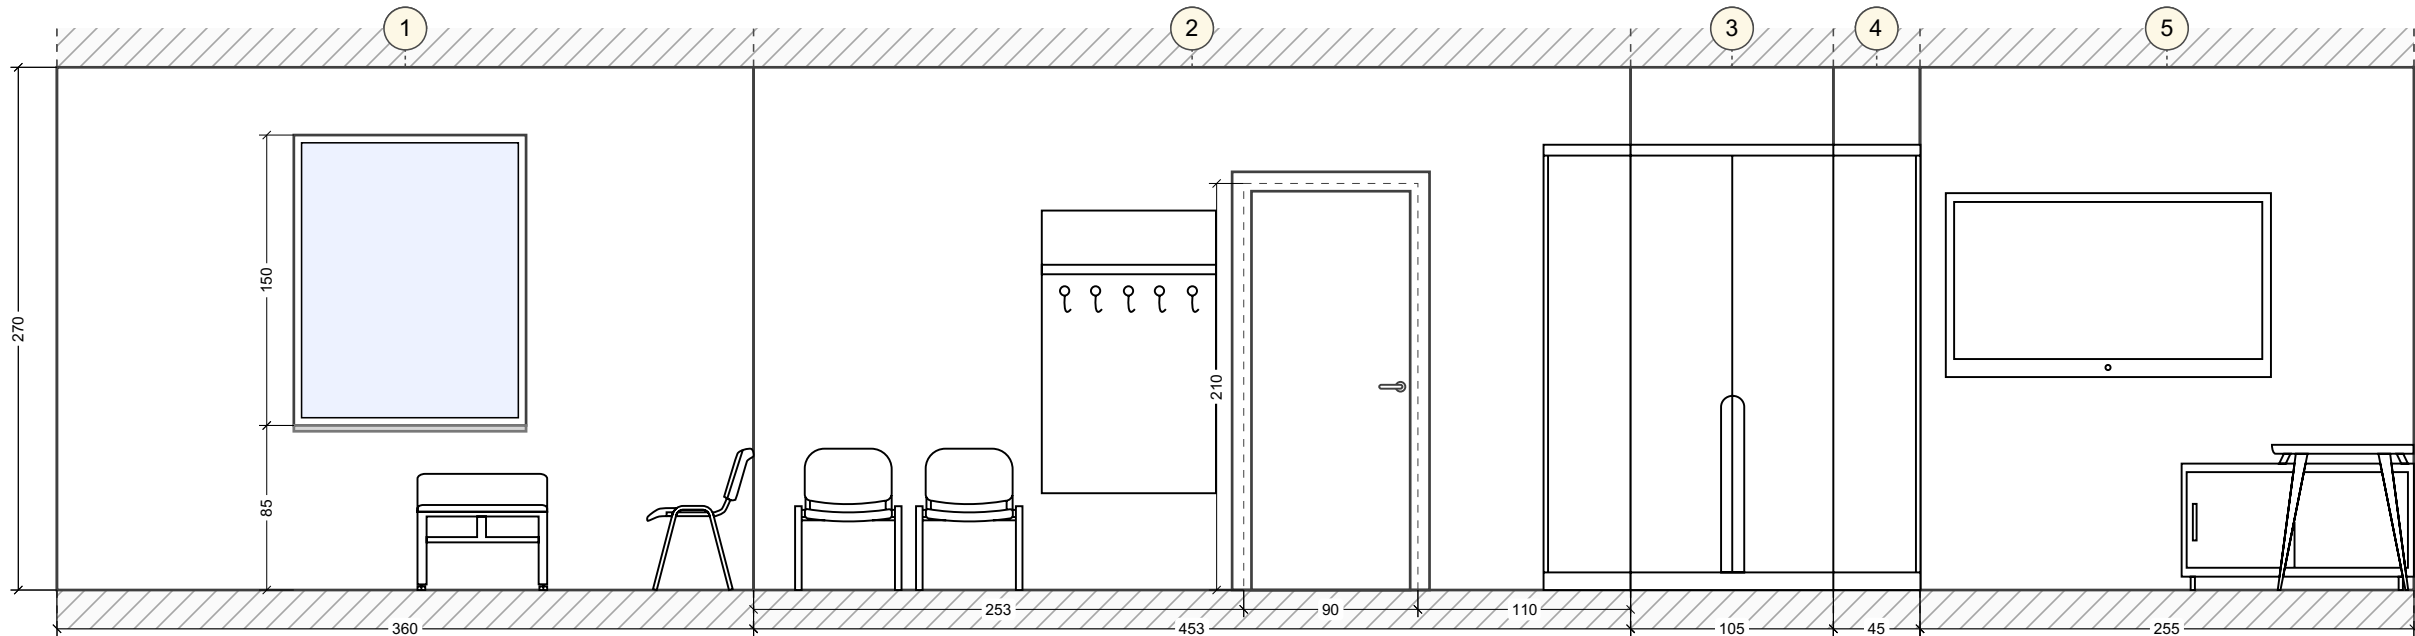


Розгортки стін. Приміщення без назви (1-4)

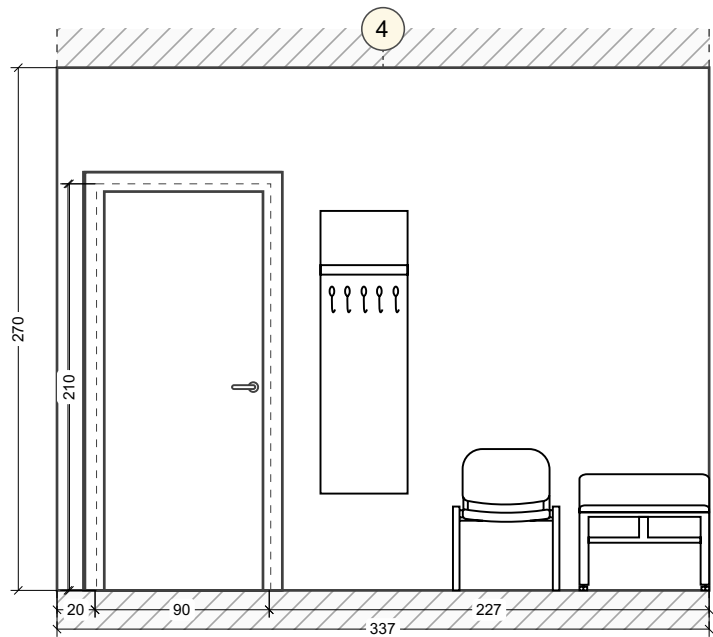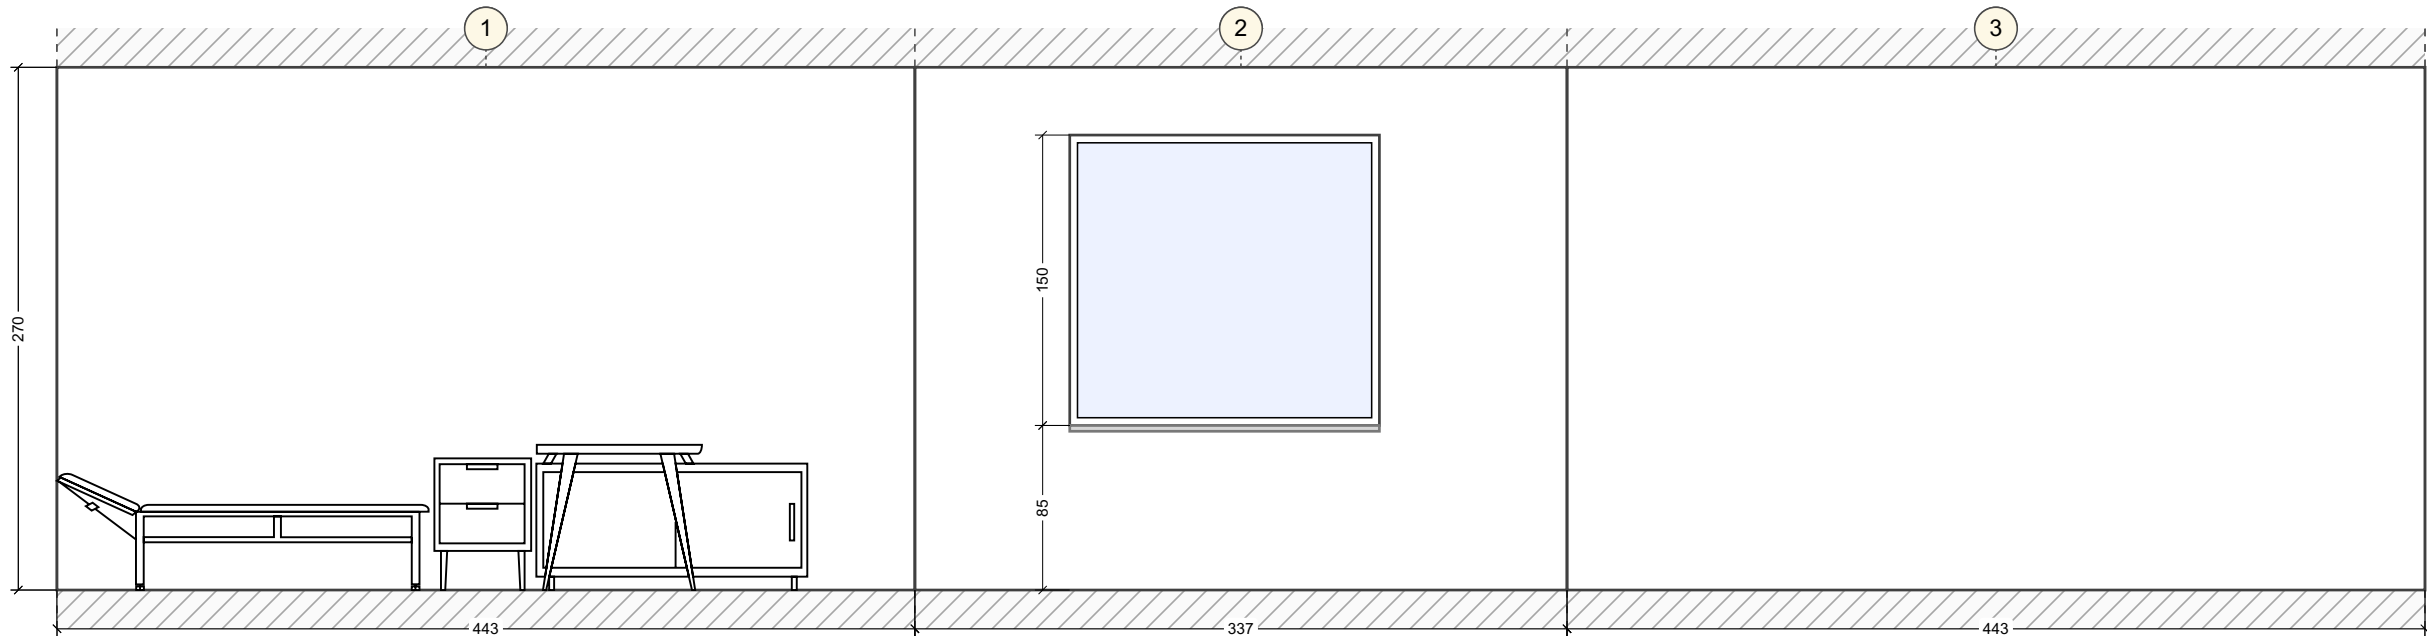






Розгортки стін. Приміщення без назви (1-4)

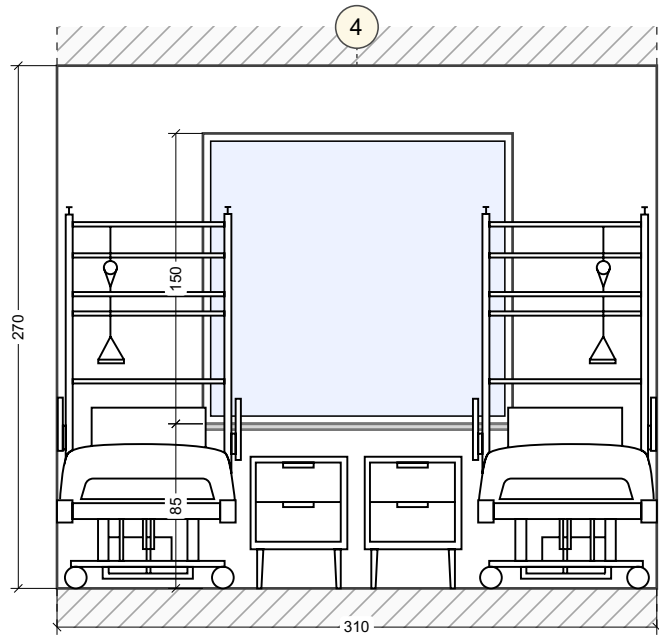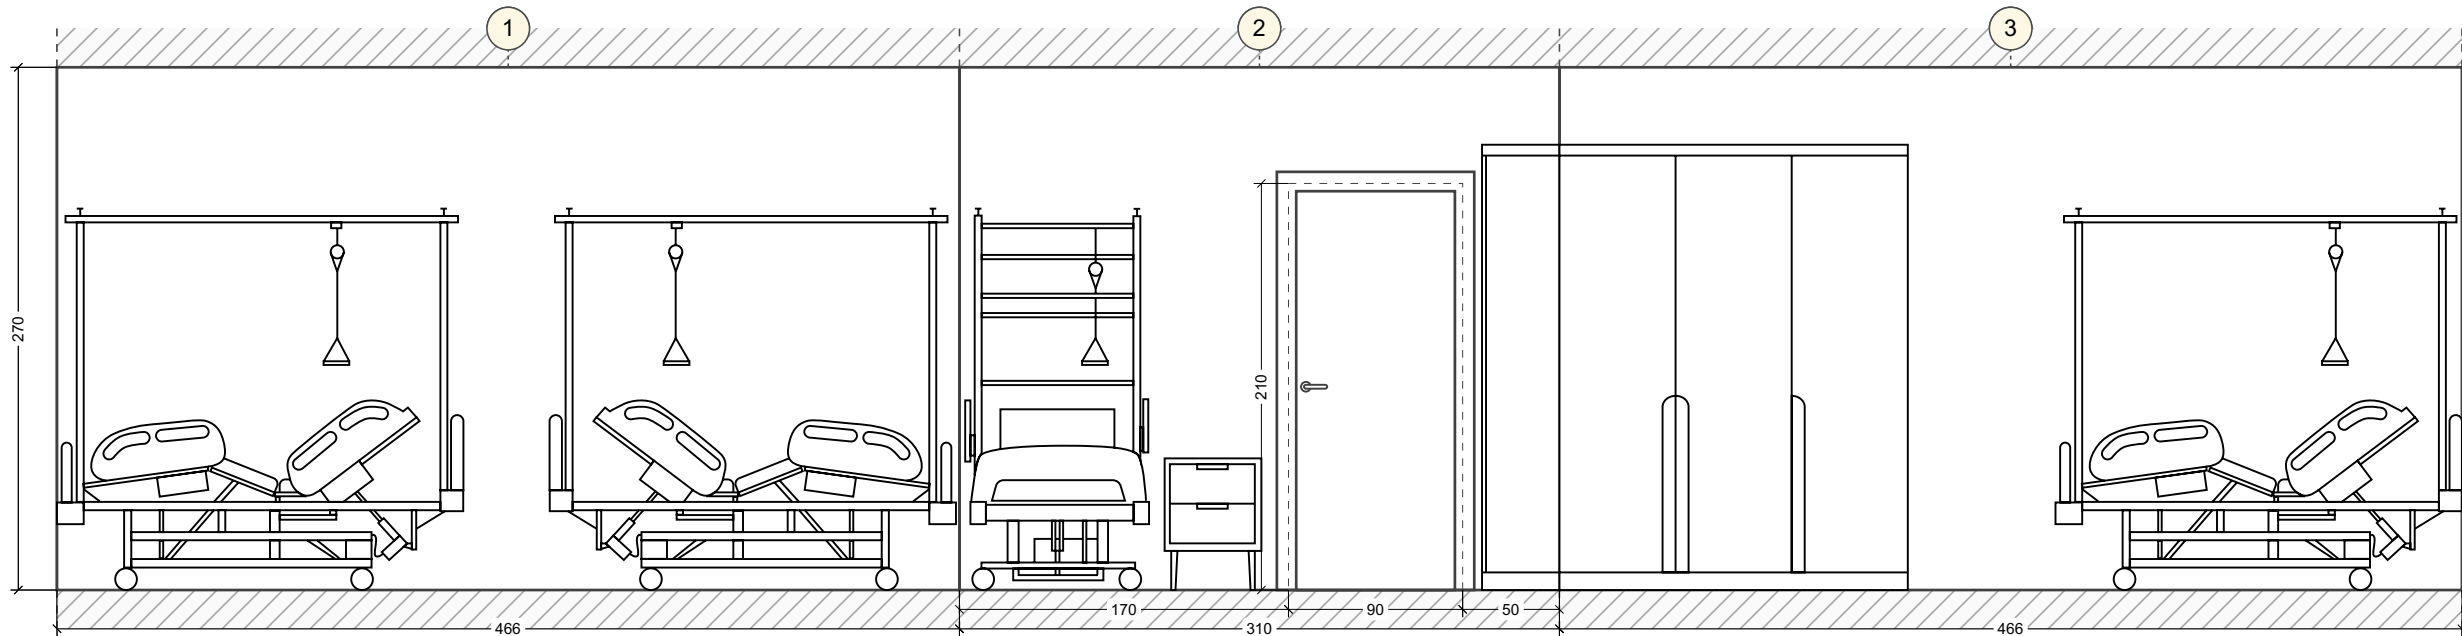


Розгортки стін. Приміщення без назви (1-4)

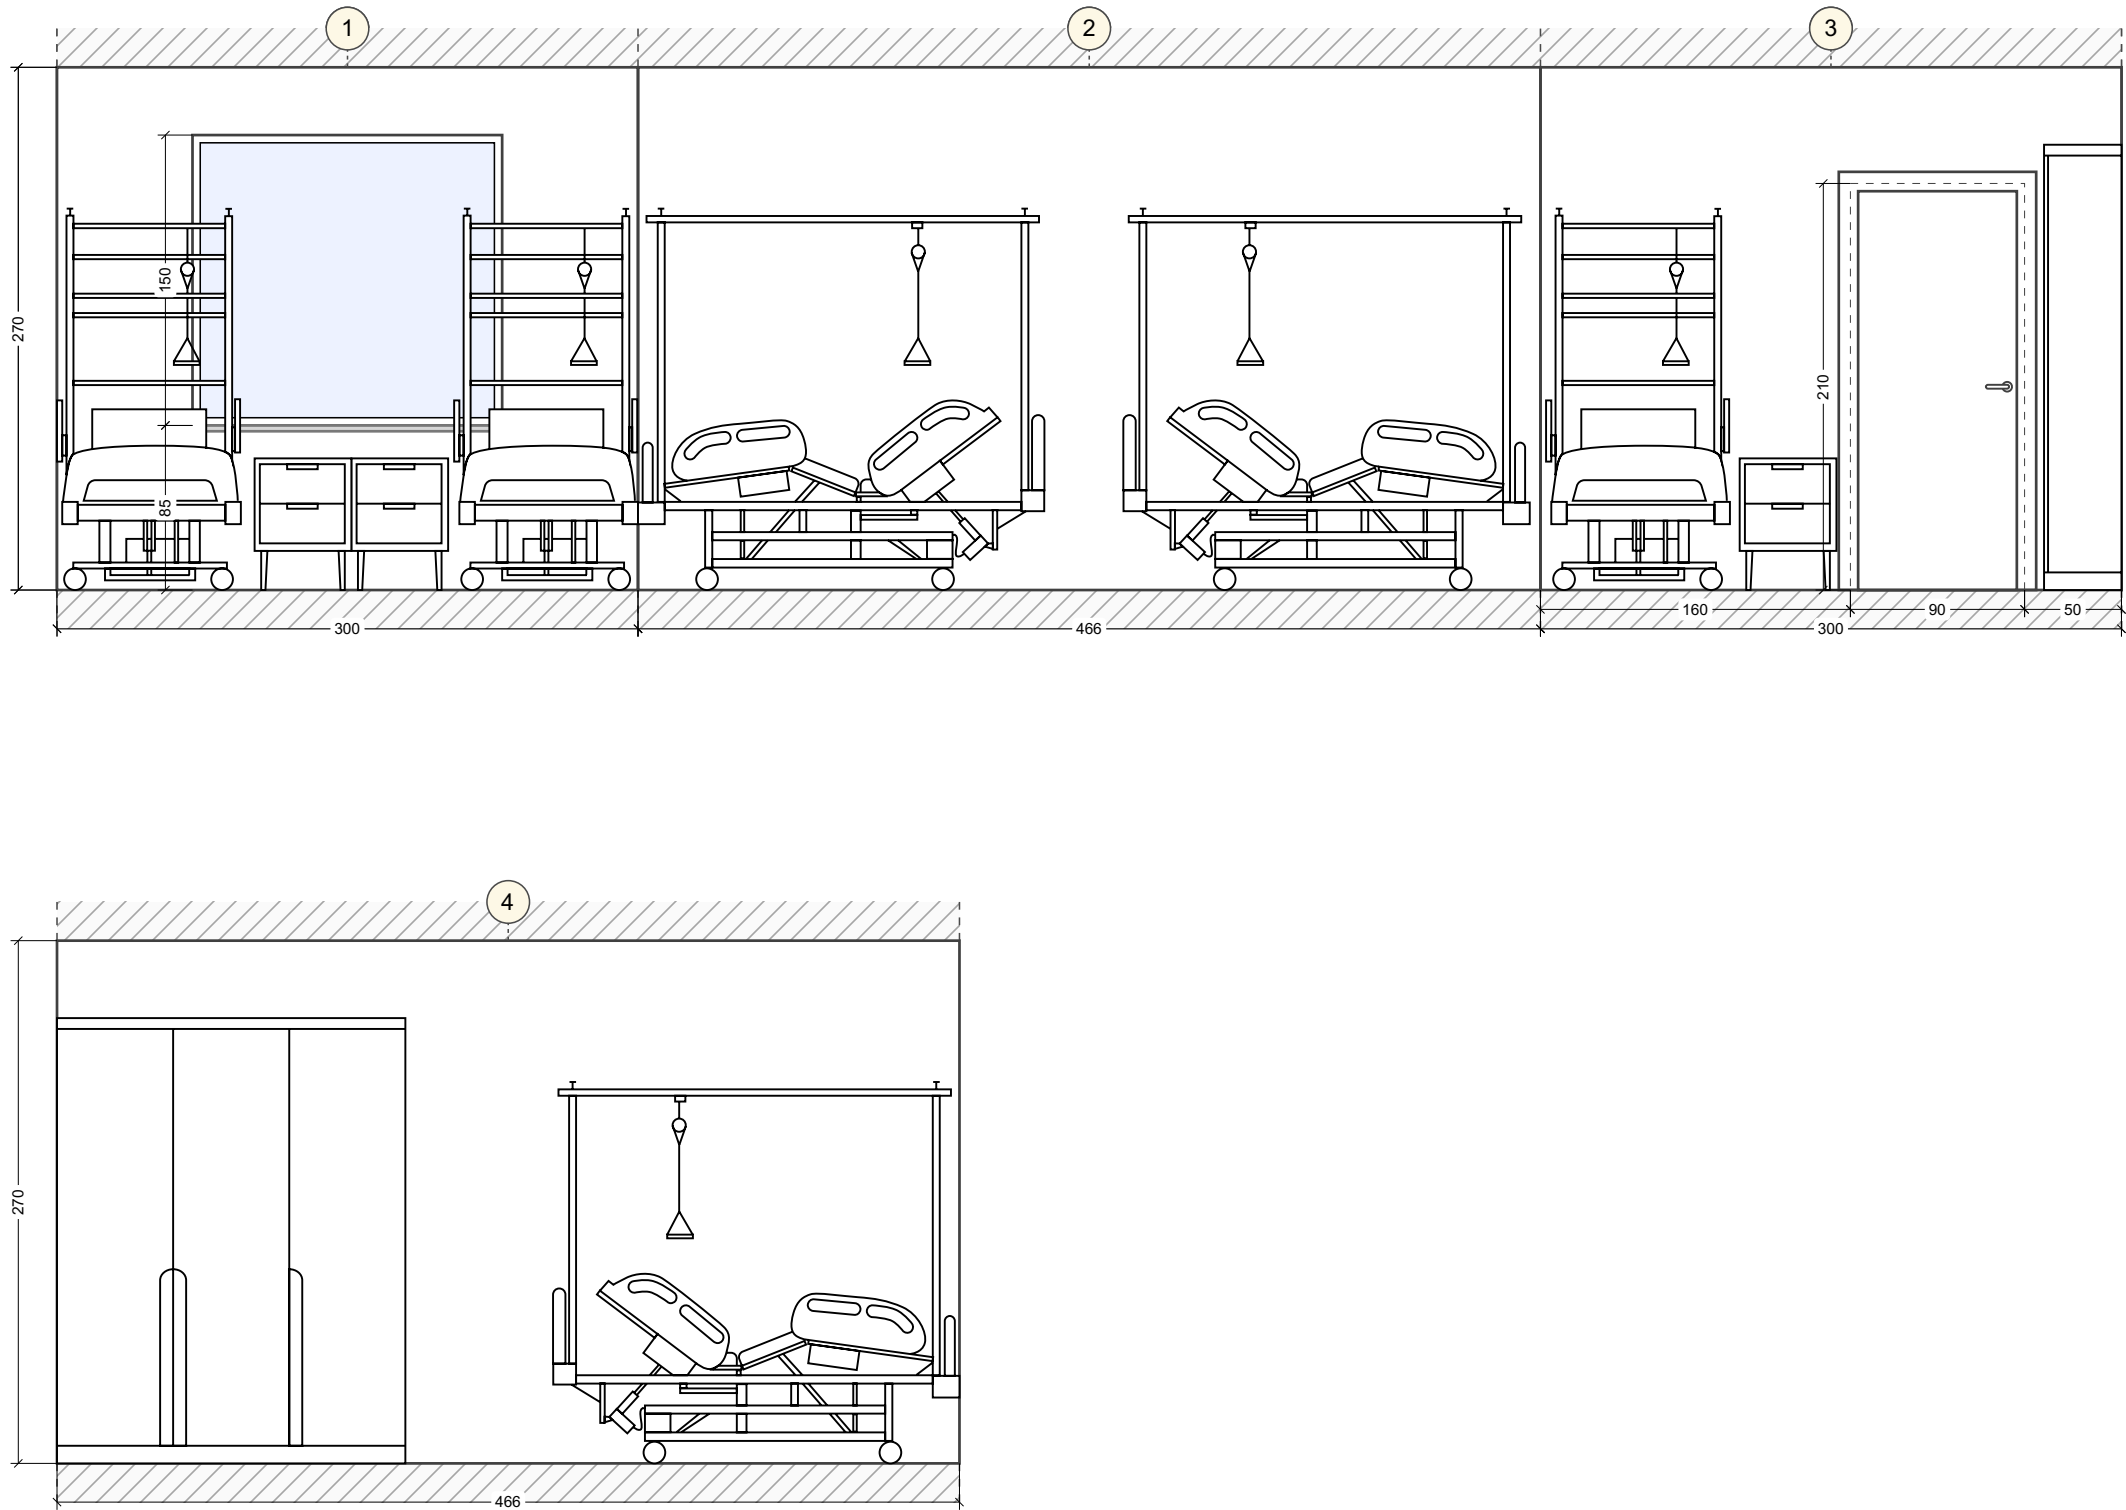


Розгортки стін. Приміщення без назви (1-4)

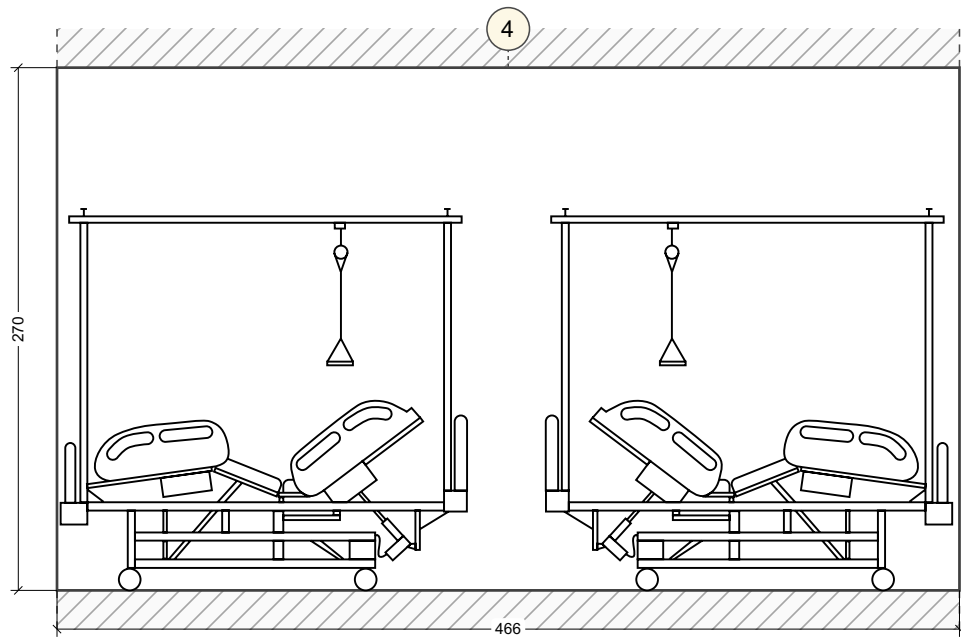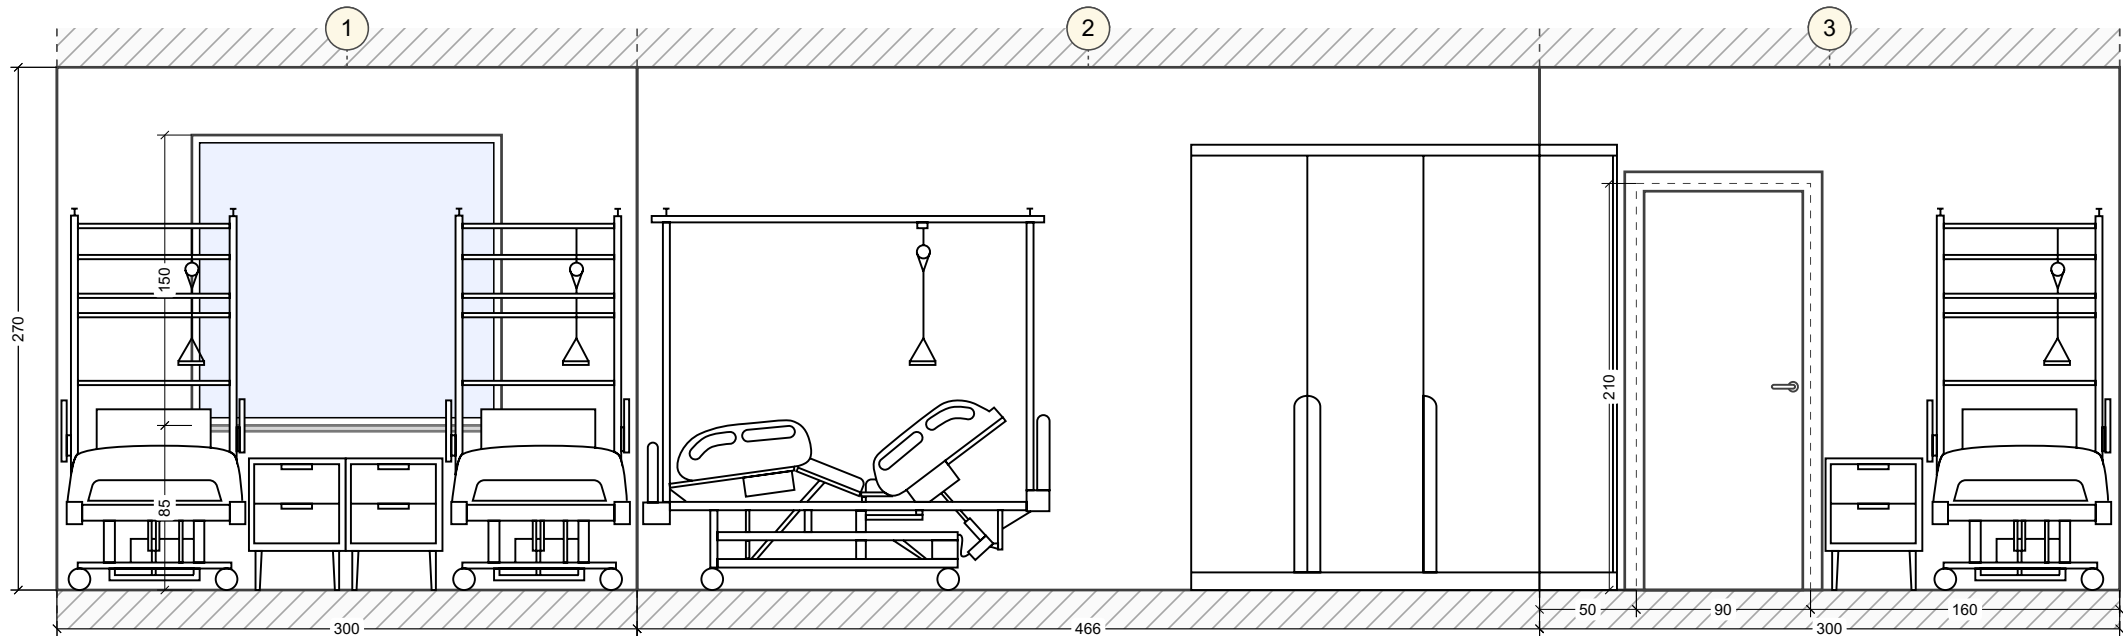


Розгортки стін. Приміщення без назви (1-4)

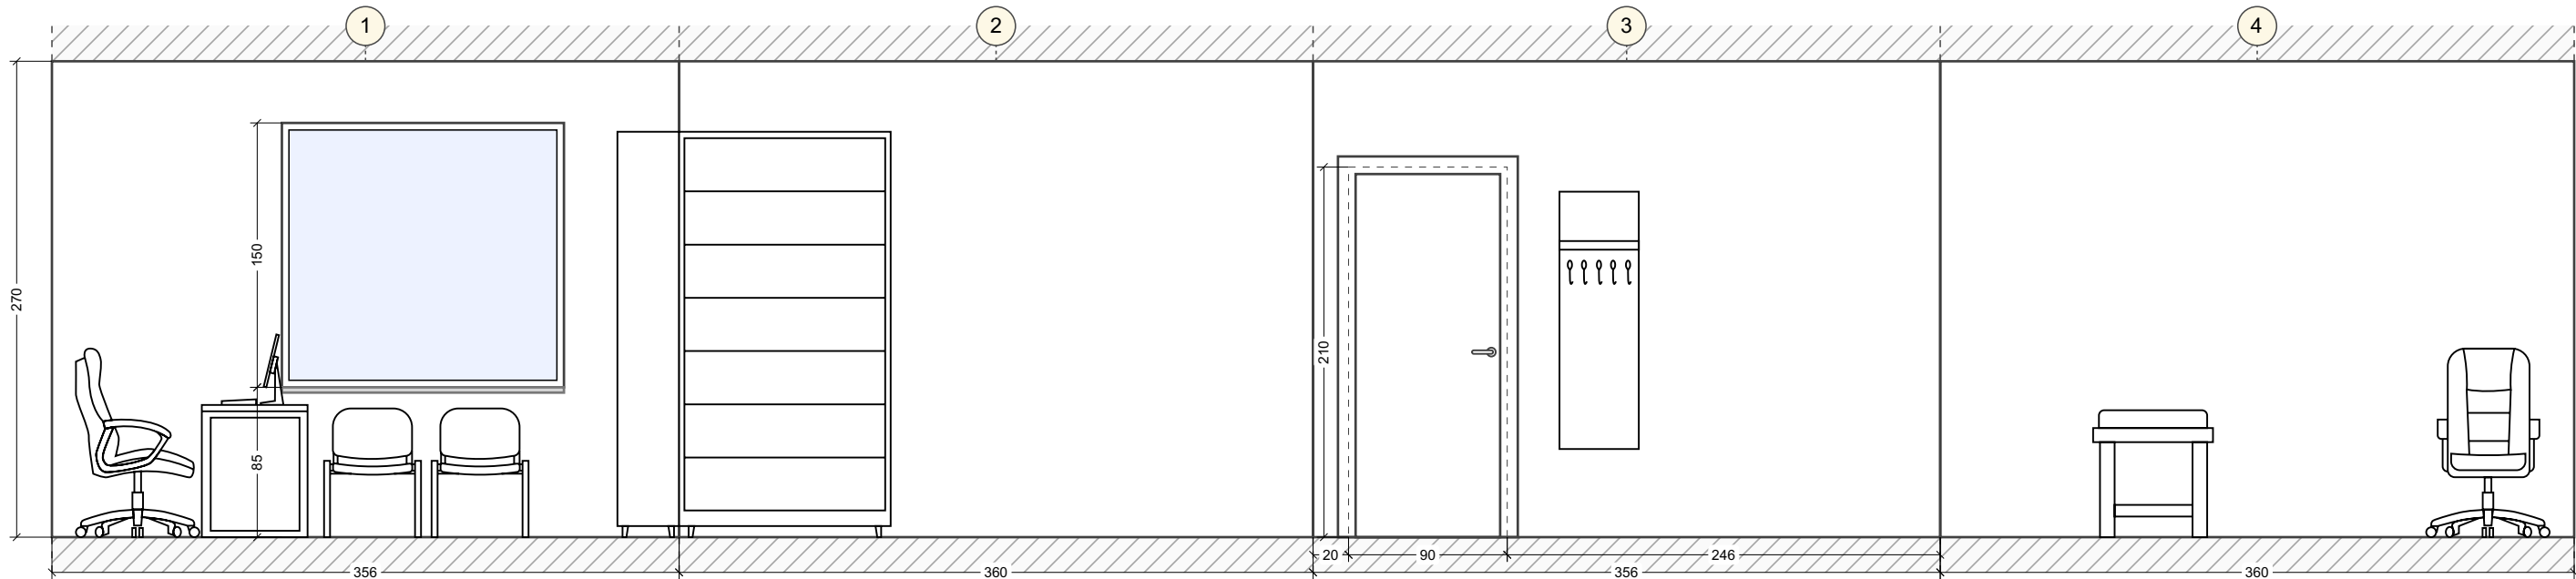

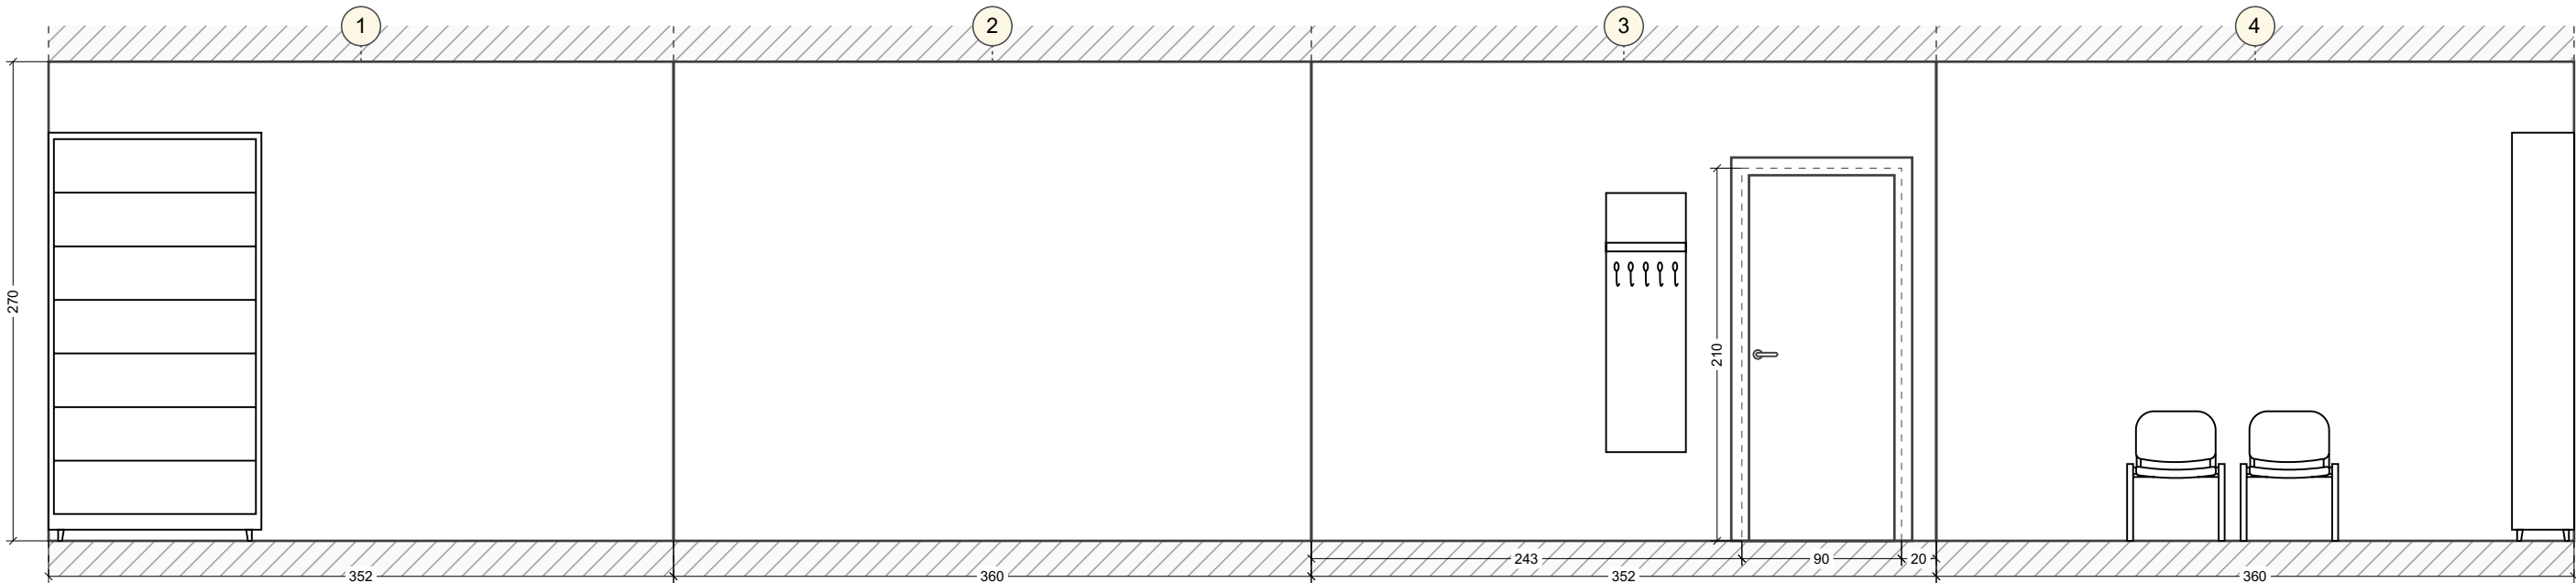


Розгортки стін. Приміщення без назви (1-4)

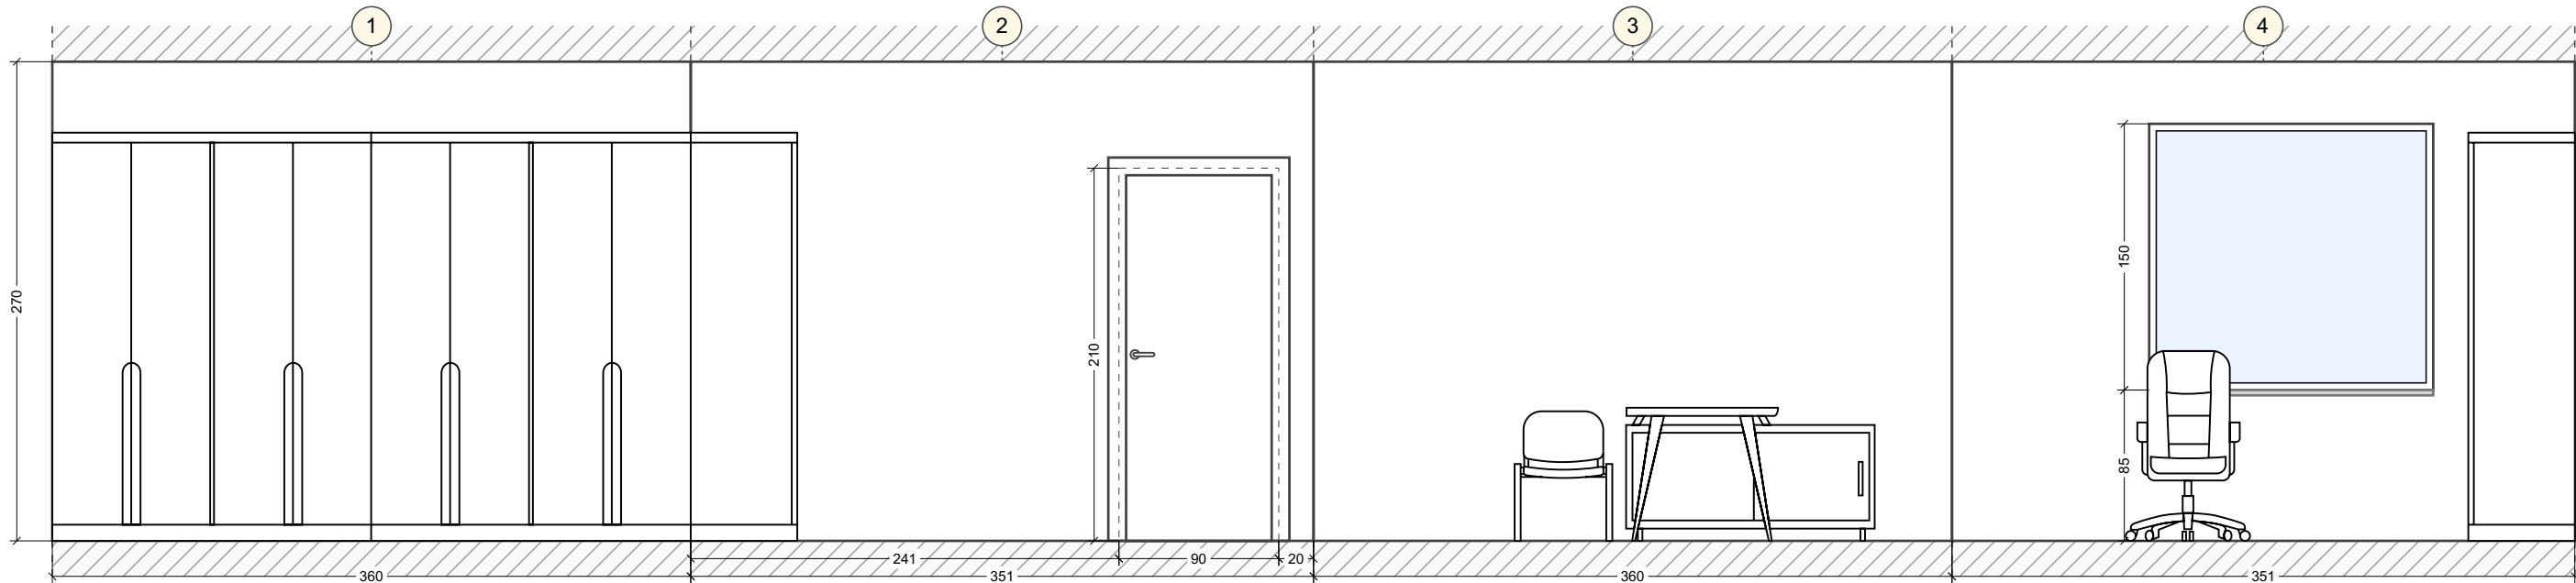




Розгортки стін. Приміщення без назви (1-4)

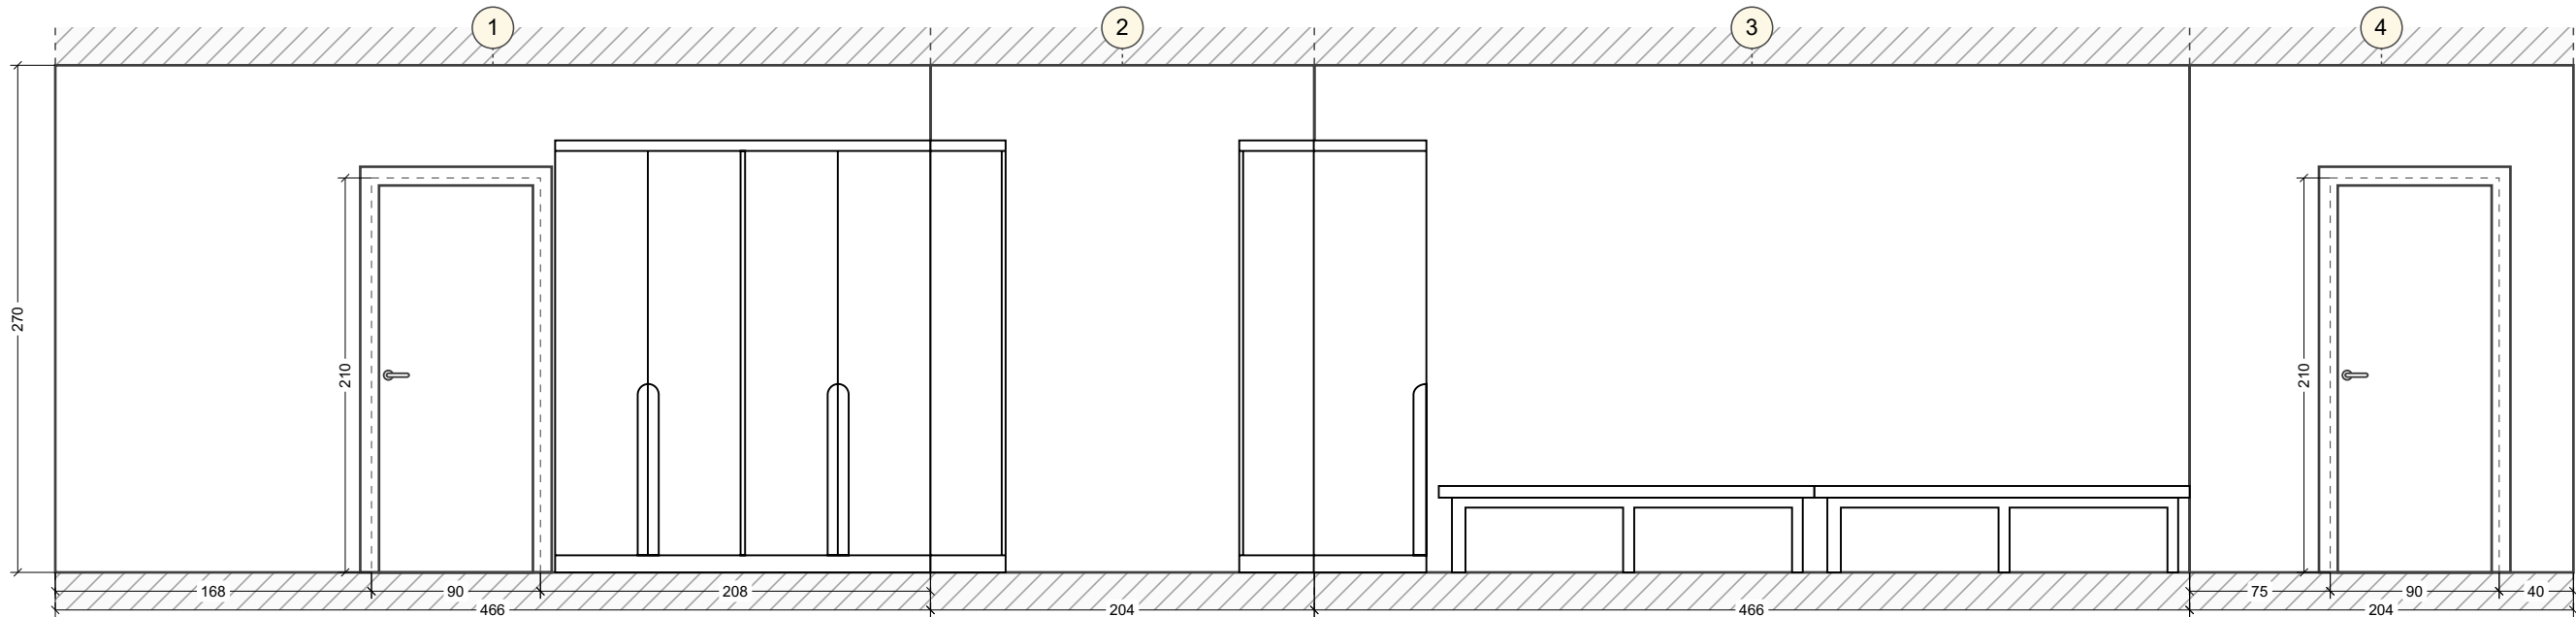


Розгортки стін. Приміщення без назви (1-4)

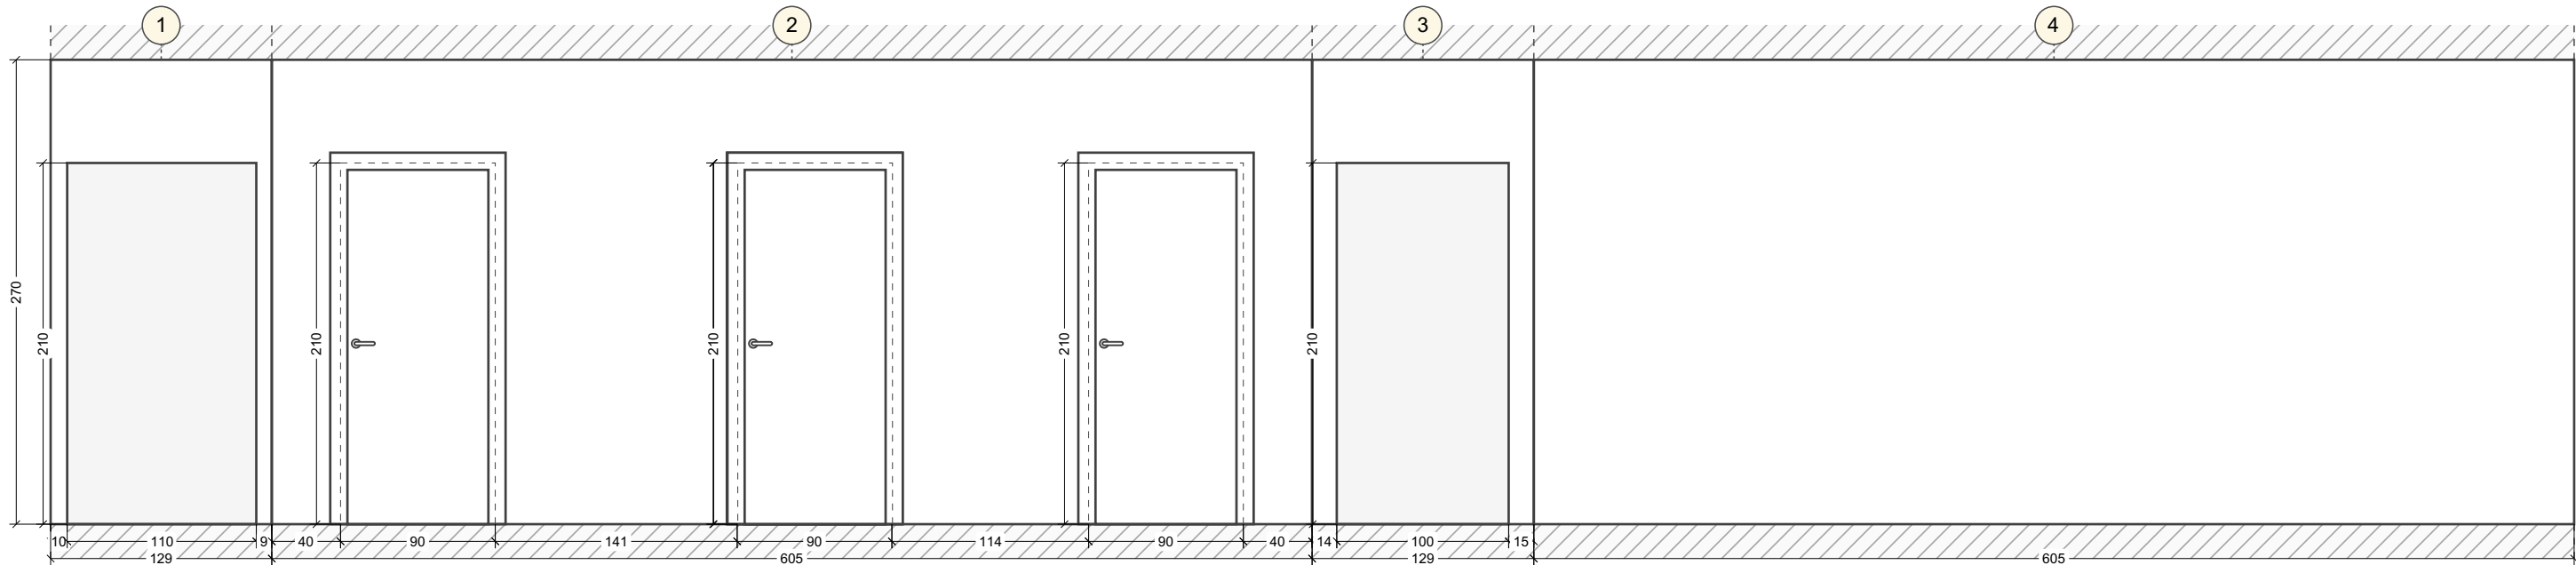





Розгортки стін. Приміщення без назви (1-4)

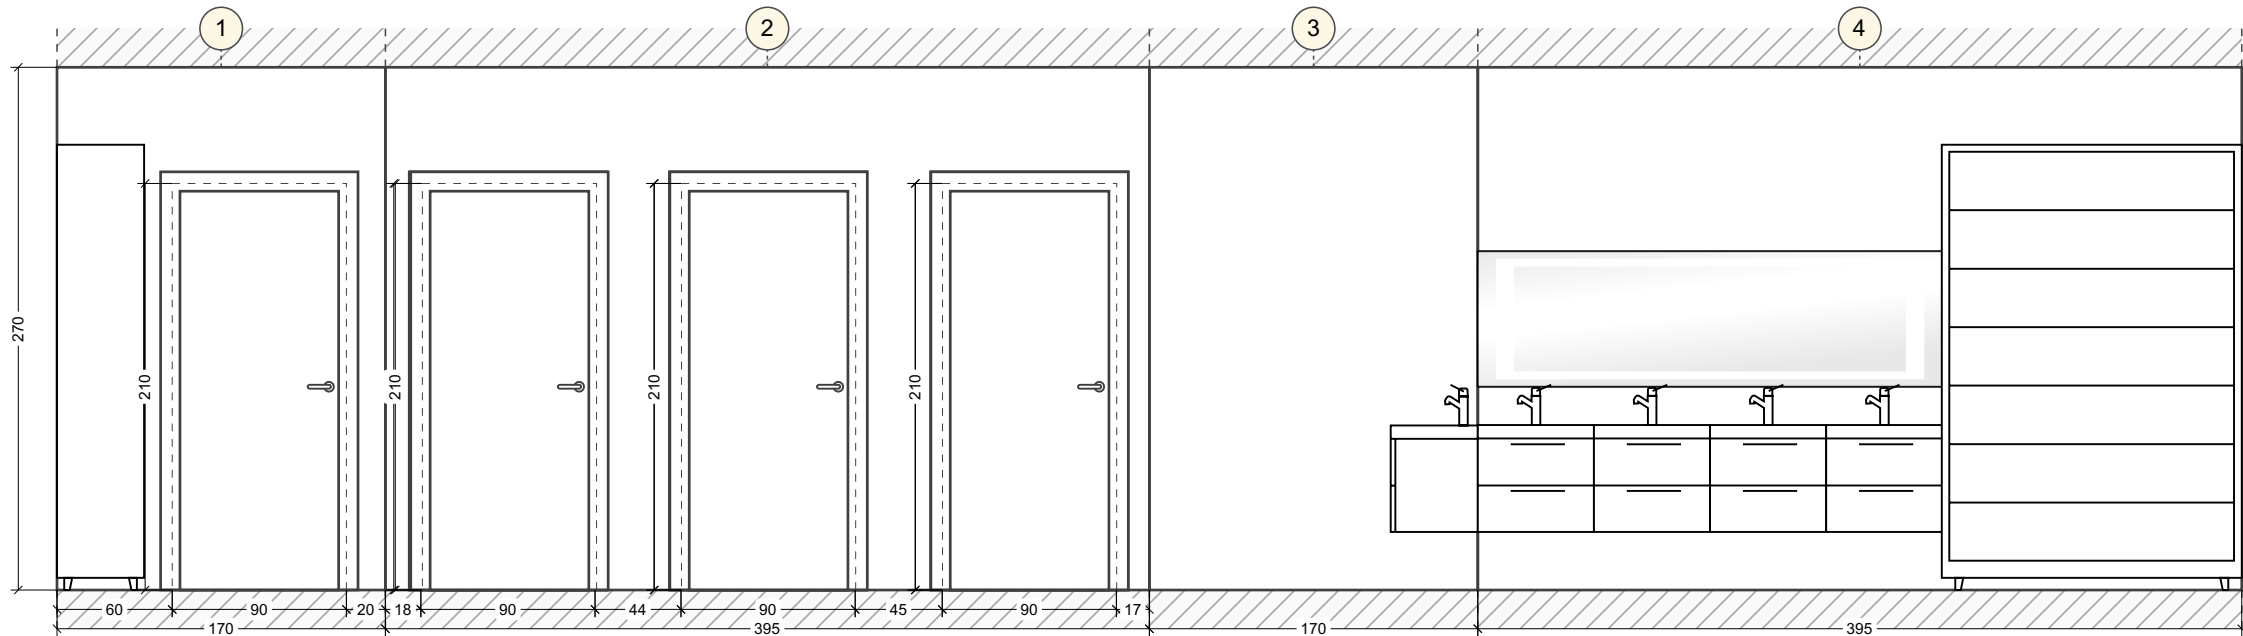


Розгортки стін. Приміщення без назви (1-4)

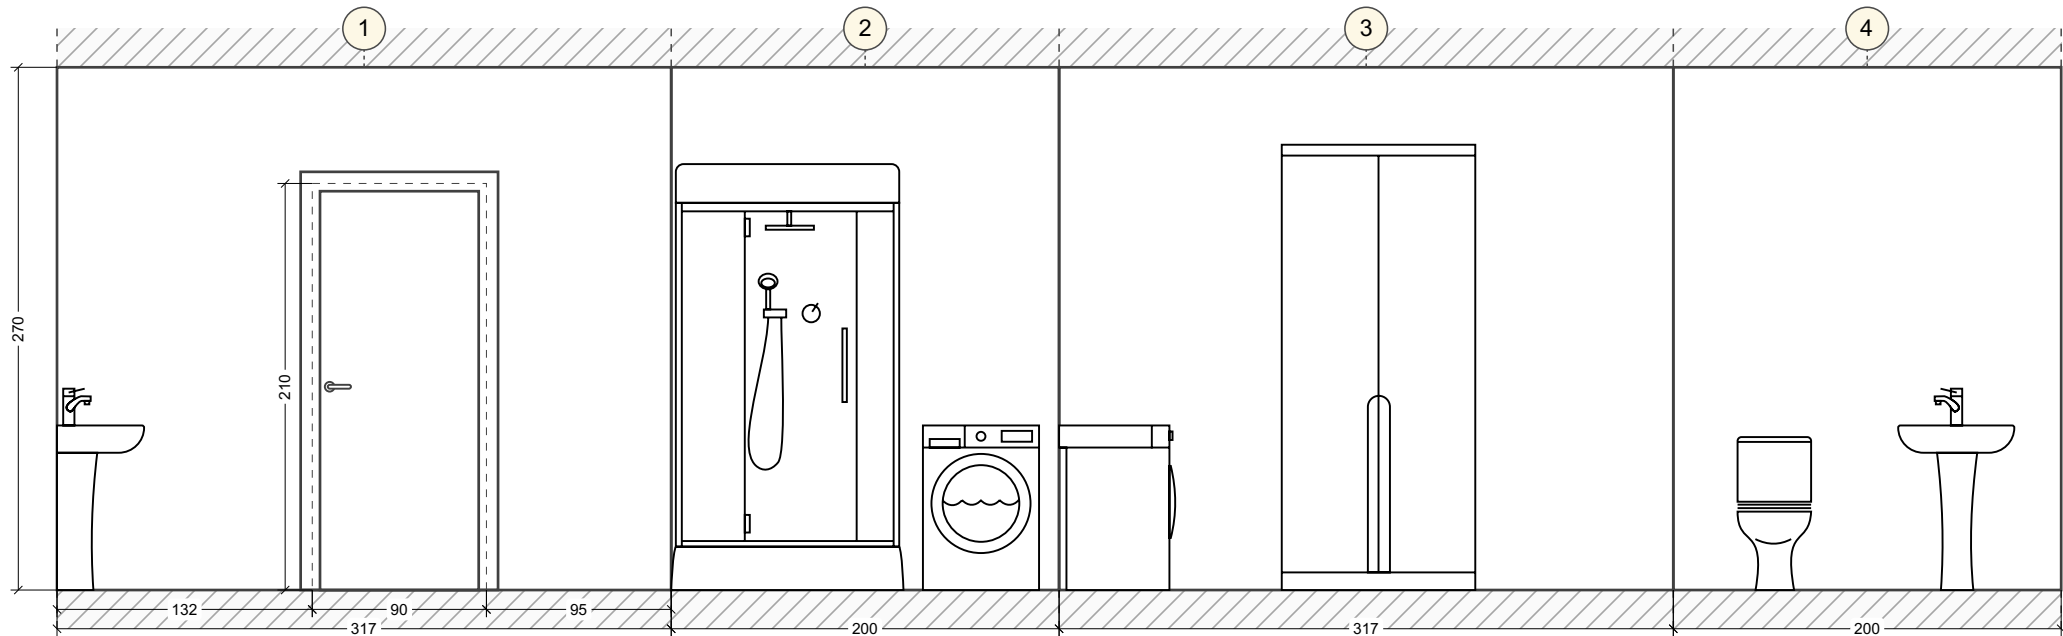


Розгортки стін. Приміщення без назви (1-4)

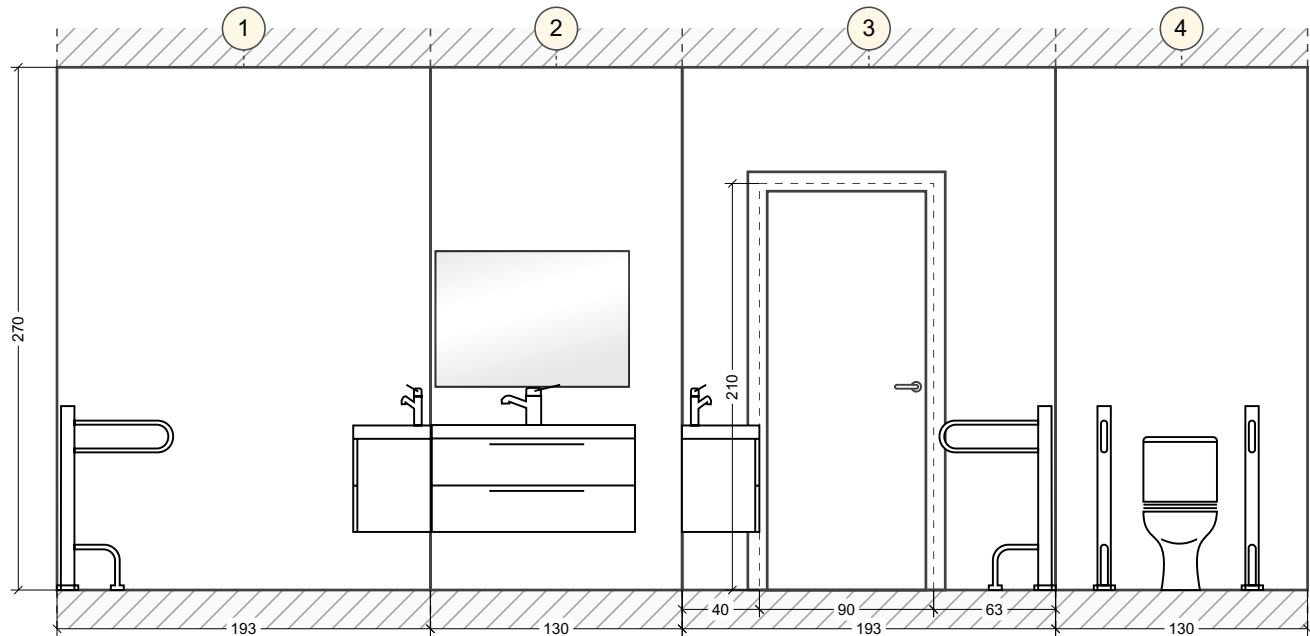


Розгортки стін. Приміщення без назви (1-6)

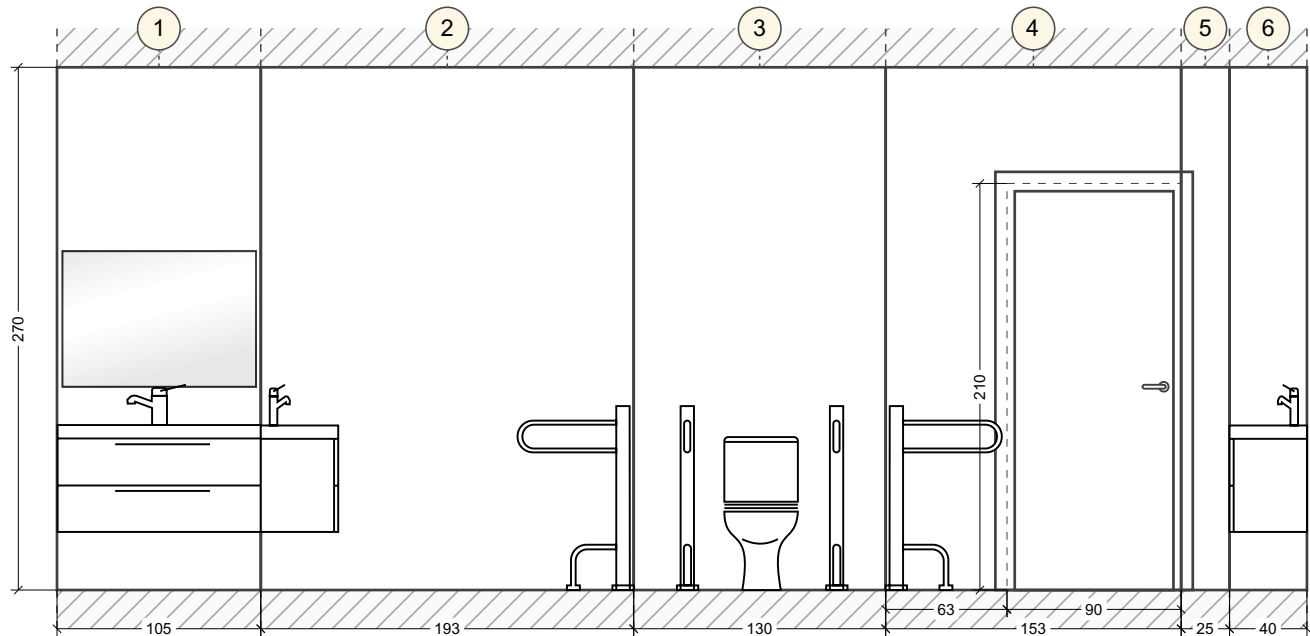

Розгортки стін. Приміщення без назви (1-6)

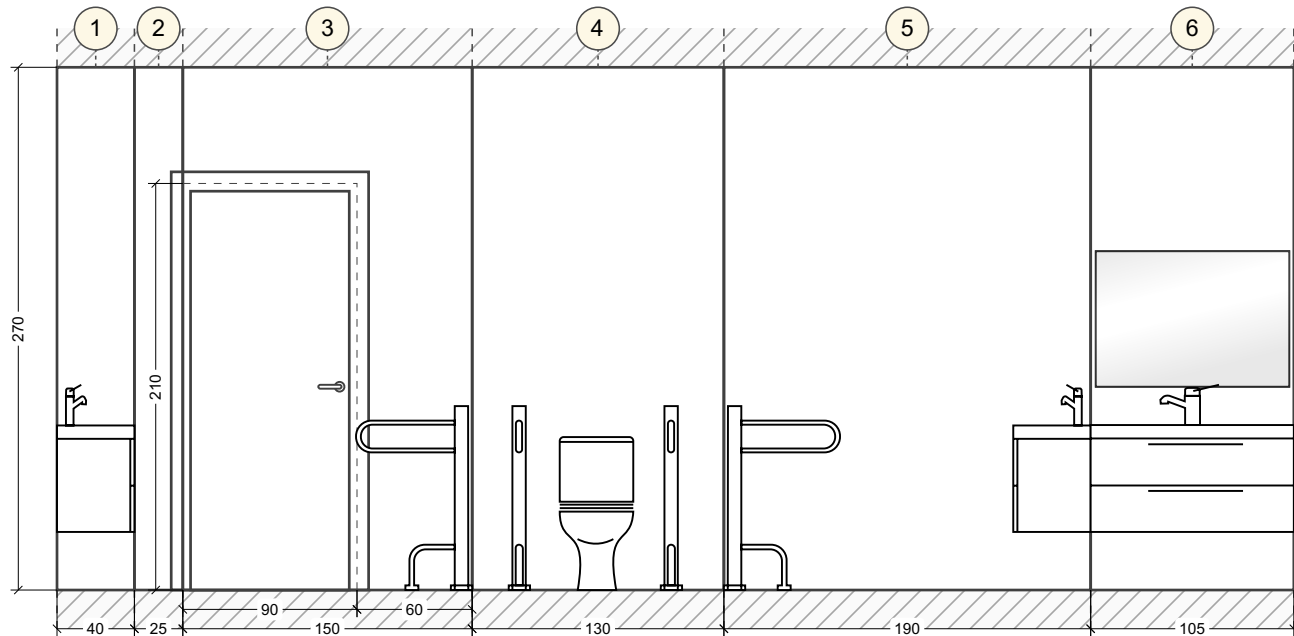


Розгортки стін. Приміщення без назви (1-4)

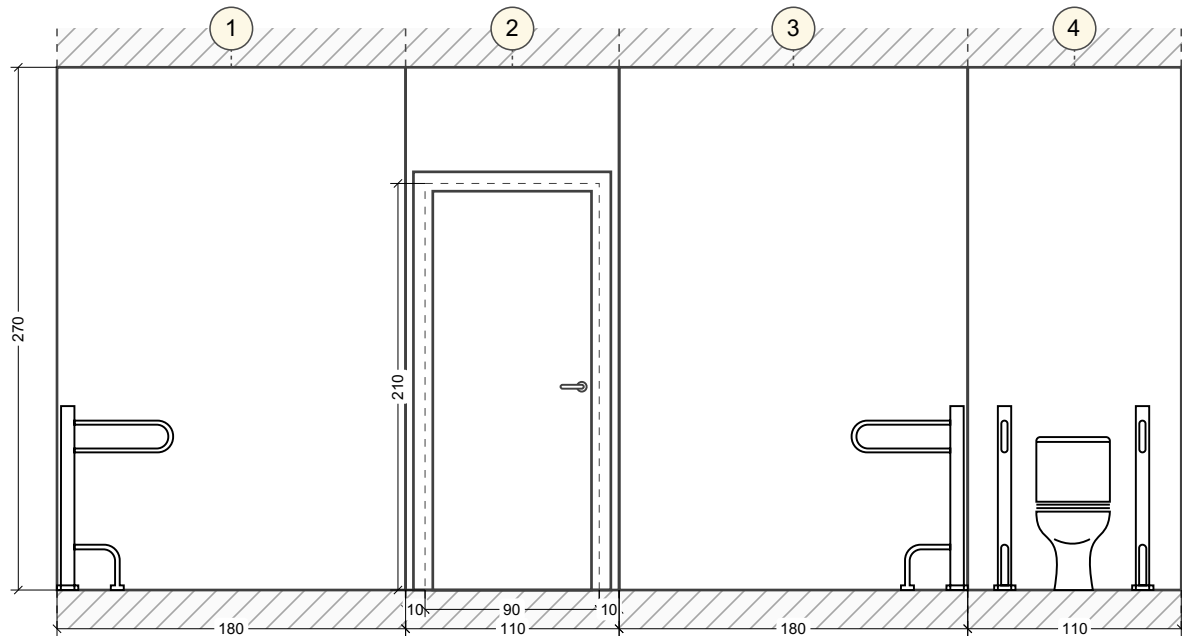




Розгортки стін. Приміщення без назви (1-4)

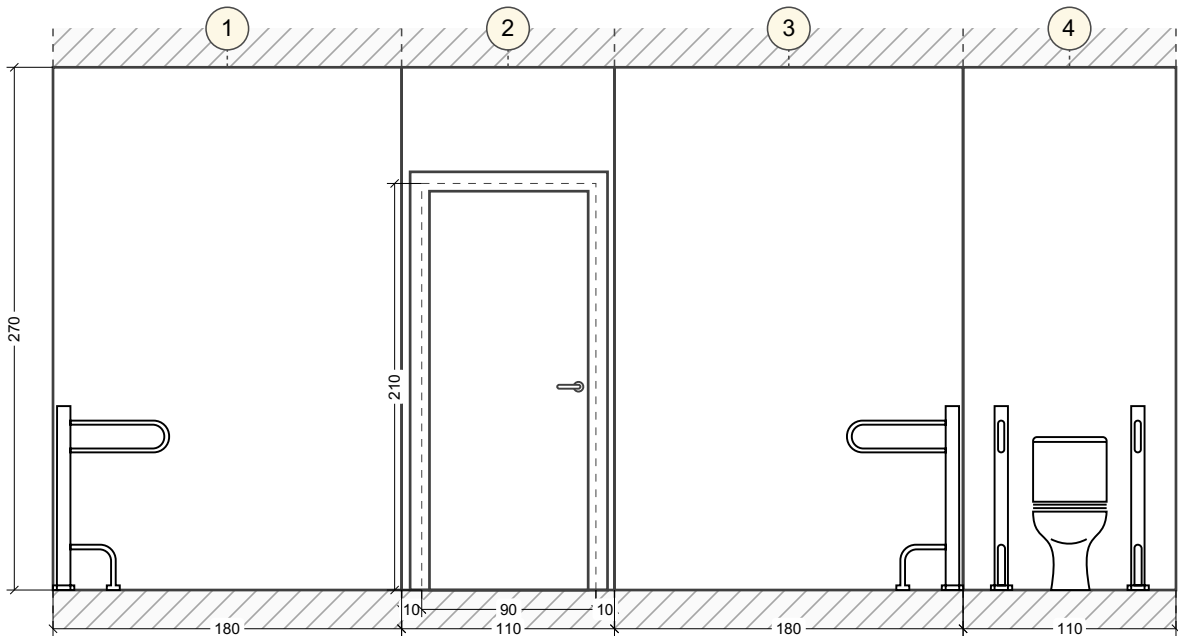


Розгортки стін. Приміщення без назви (1-4)

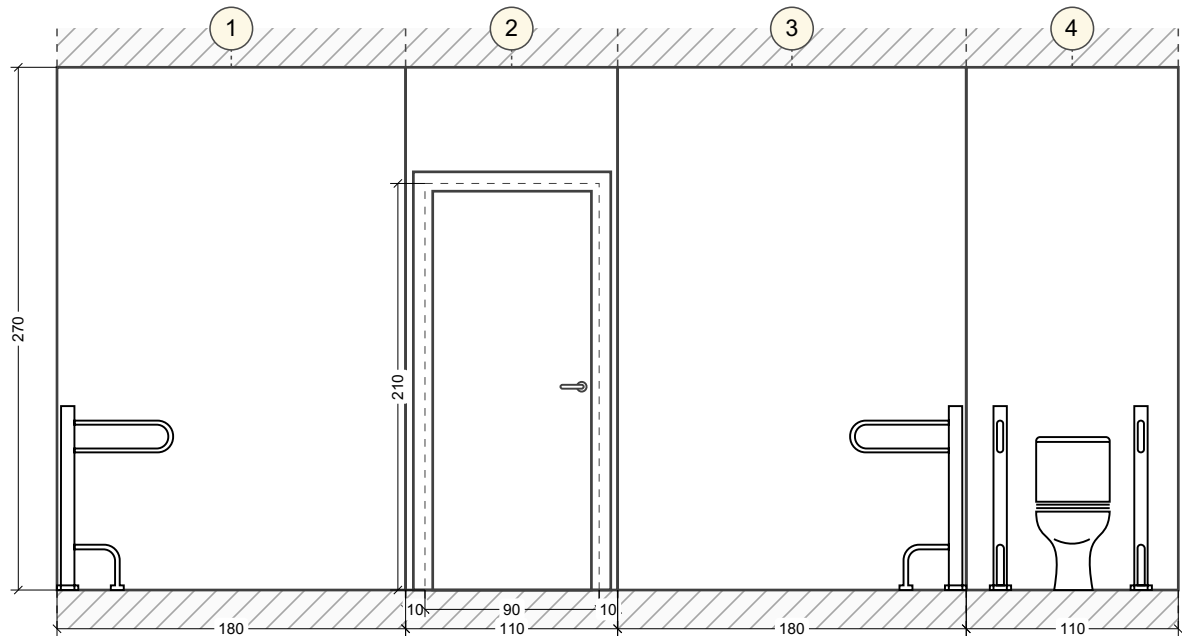




Розгортки стін. Приміщення без назви (1-4)

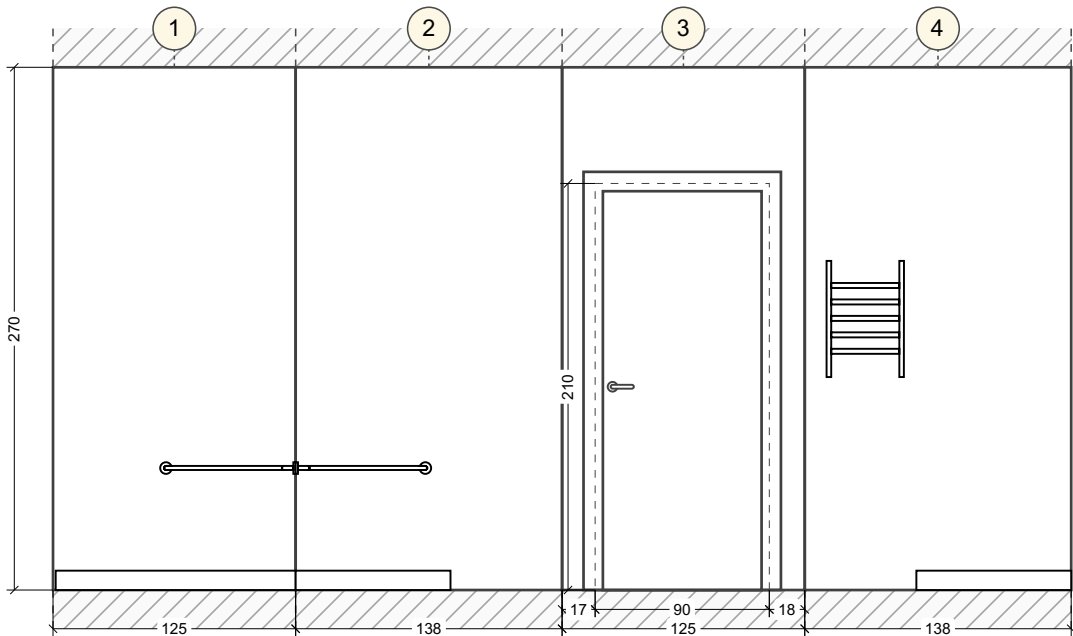

Розгортки стін. Приміщення без назви (1-4)

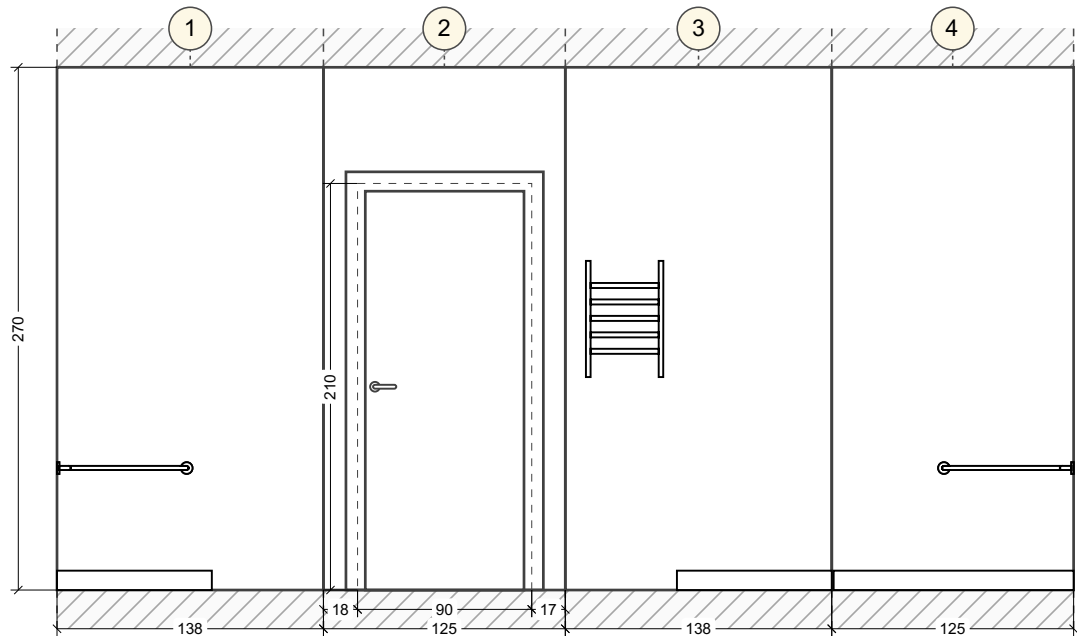

Розгортки стін. Приміщення без назви (1-4)

